07号平面｜总图01_儿科急诊｜标注草稿：候选均待确认

共 39 项；核对号先左栏后右栏，各栏自上而下；按“01=名称，02=名称”分批回复。

边栏：核对号｜S编号｜候选用途（把握程度）；依据见同目录核对清单。原图未改动。

01｜S002｜儿科急诊｜候选：办公室 / 值班室（低）
02｜S004｜儿科急诊｜候选：工作人员支持用房（低）
03｜S006｜儿科急诊｜候选：工作人员支持用房（低）
04｜S008｜儿科急诊｜候选：库房 / 设备用房（低）
05｜S010｜儿科急诊｜候选：挂号收费 / 服务用房（低）
06｜S013｜儿科急诊｜候选：挂号收费 / 服务用房（低）
07｜S015｜儿科急诊｜候选：抢救室 / 留观室（中）
08｜S017｜儿科急诊｜候选：工作人员支持用房（低）
09｜S016｜儿科急诊｜候选：工作人员支持用房（低）
10｜S018｜儿科急诊｜候选：卫生间 / 更衣室（低）
11｜S019｜儿科急诊｜候选：B超检查室 / 诊室（低）
12｜S020｜儿科急诊｜候选：检查室 / 处置室（低）
13｜S021｜儿科急诊｜候选：检查室 / 处置室（低）
14｜S023｜儿科急诊｜候选：卫生间 / 更衣室（低）
15｜S024｜儿科急诊｜候选：库房 / 设备用房（低）
16｜S025｜儿科急诊｜候选：留观室 / 治疗室（低）
17｜S026｜儿科急诊｜候选：检查室 / 处置室（低）
18｜S028｜儿科急诊｜候选：儿科诊室 / 检查室（低）
19｜S029｜儿科急诊｜候选：患者准备 / 支持用房（低）
20｜S030｜儿科急诊｜候选：库房 / 设备用房（低）
21｜S031｜儿科急诊｜候选：库房 / 设备用房（低）
22｜S032｜儿科急诊｜候选：工作人员支持用房（低）
23｜S034｜儿科急诊｜候选：检查室 / 处置室（低）
24｜S035｜儿科急诊｜候选：儿科诊室 / 检查室（低）
25｜S036｜儿科急诊｜候选：观察室 / 留观室（中）
26｜S033｜儿科急诊｜候选：留观室 / 治疗室（低）
27｜S037｜儿科急诊｜候选：检查室 / 处置室（低）
28｜S038｜儿科急诊｜候选：儿科诊室 / 检查室（低）
29｜S040｜儿科急诊｜候选：设备用房 / 库房（低）
30｜S041｜儿科急诊｜候选：检查室 / 处置室（低）
31｜S042｜儿科急诊｜候选：儿科诊室 / 检查室（低）
32｜S043｜儿科急诊｜候选：卫生间 / 更衣室（低）
33｜S044｜儿科急诊｜候选：卫生间 / 更衣室（低）
34｜S045｜儿科急诊｜候选：观察室 / 留观室（中）
35｜S046｜儿科急诊｜候选：诊室 / 检查室（低）
36｜S047｜儿科急诊｜候选：处置室 / 治疗室（低）
37｜S048｜儿科急诊｜候选：心电图室 / 检查室（低）
38｜S049｜儿科急诊｜候选：治疗室 / 处置室（低）
39｜S050｜儿科急诊｜候选：诊室 / 检查室（低）

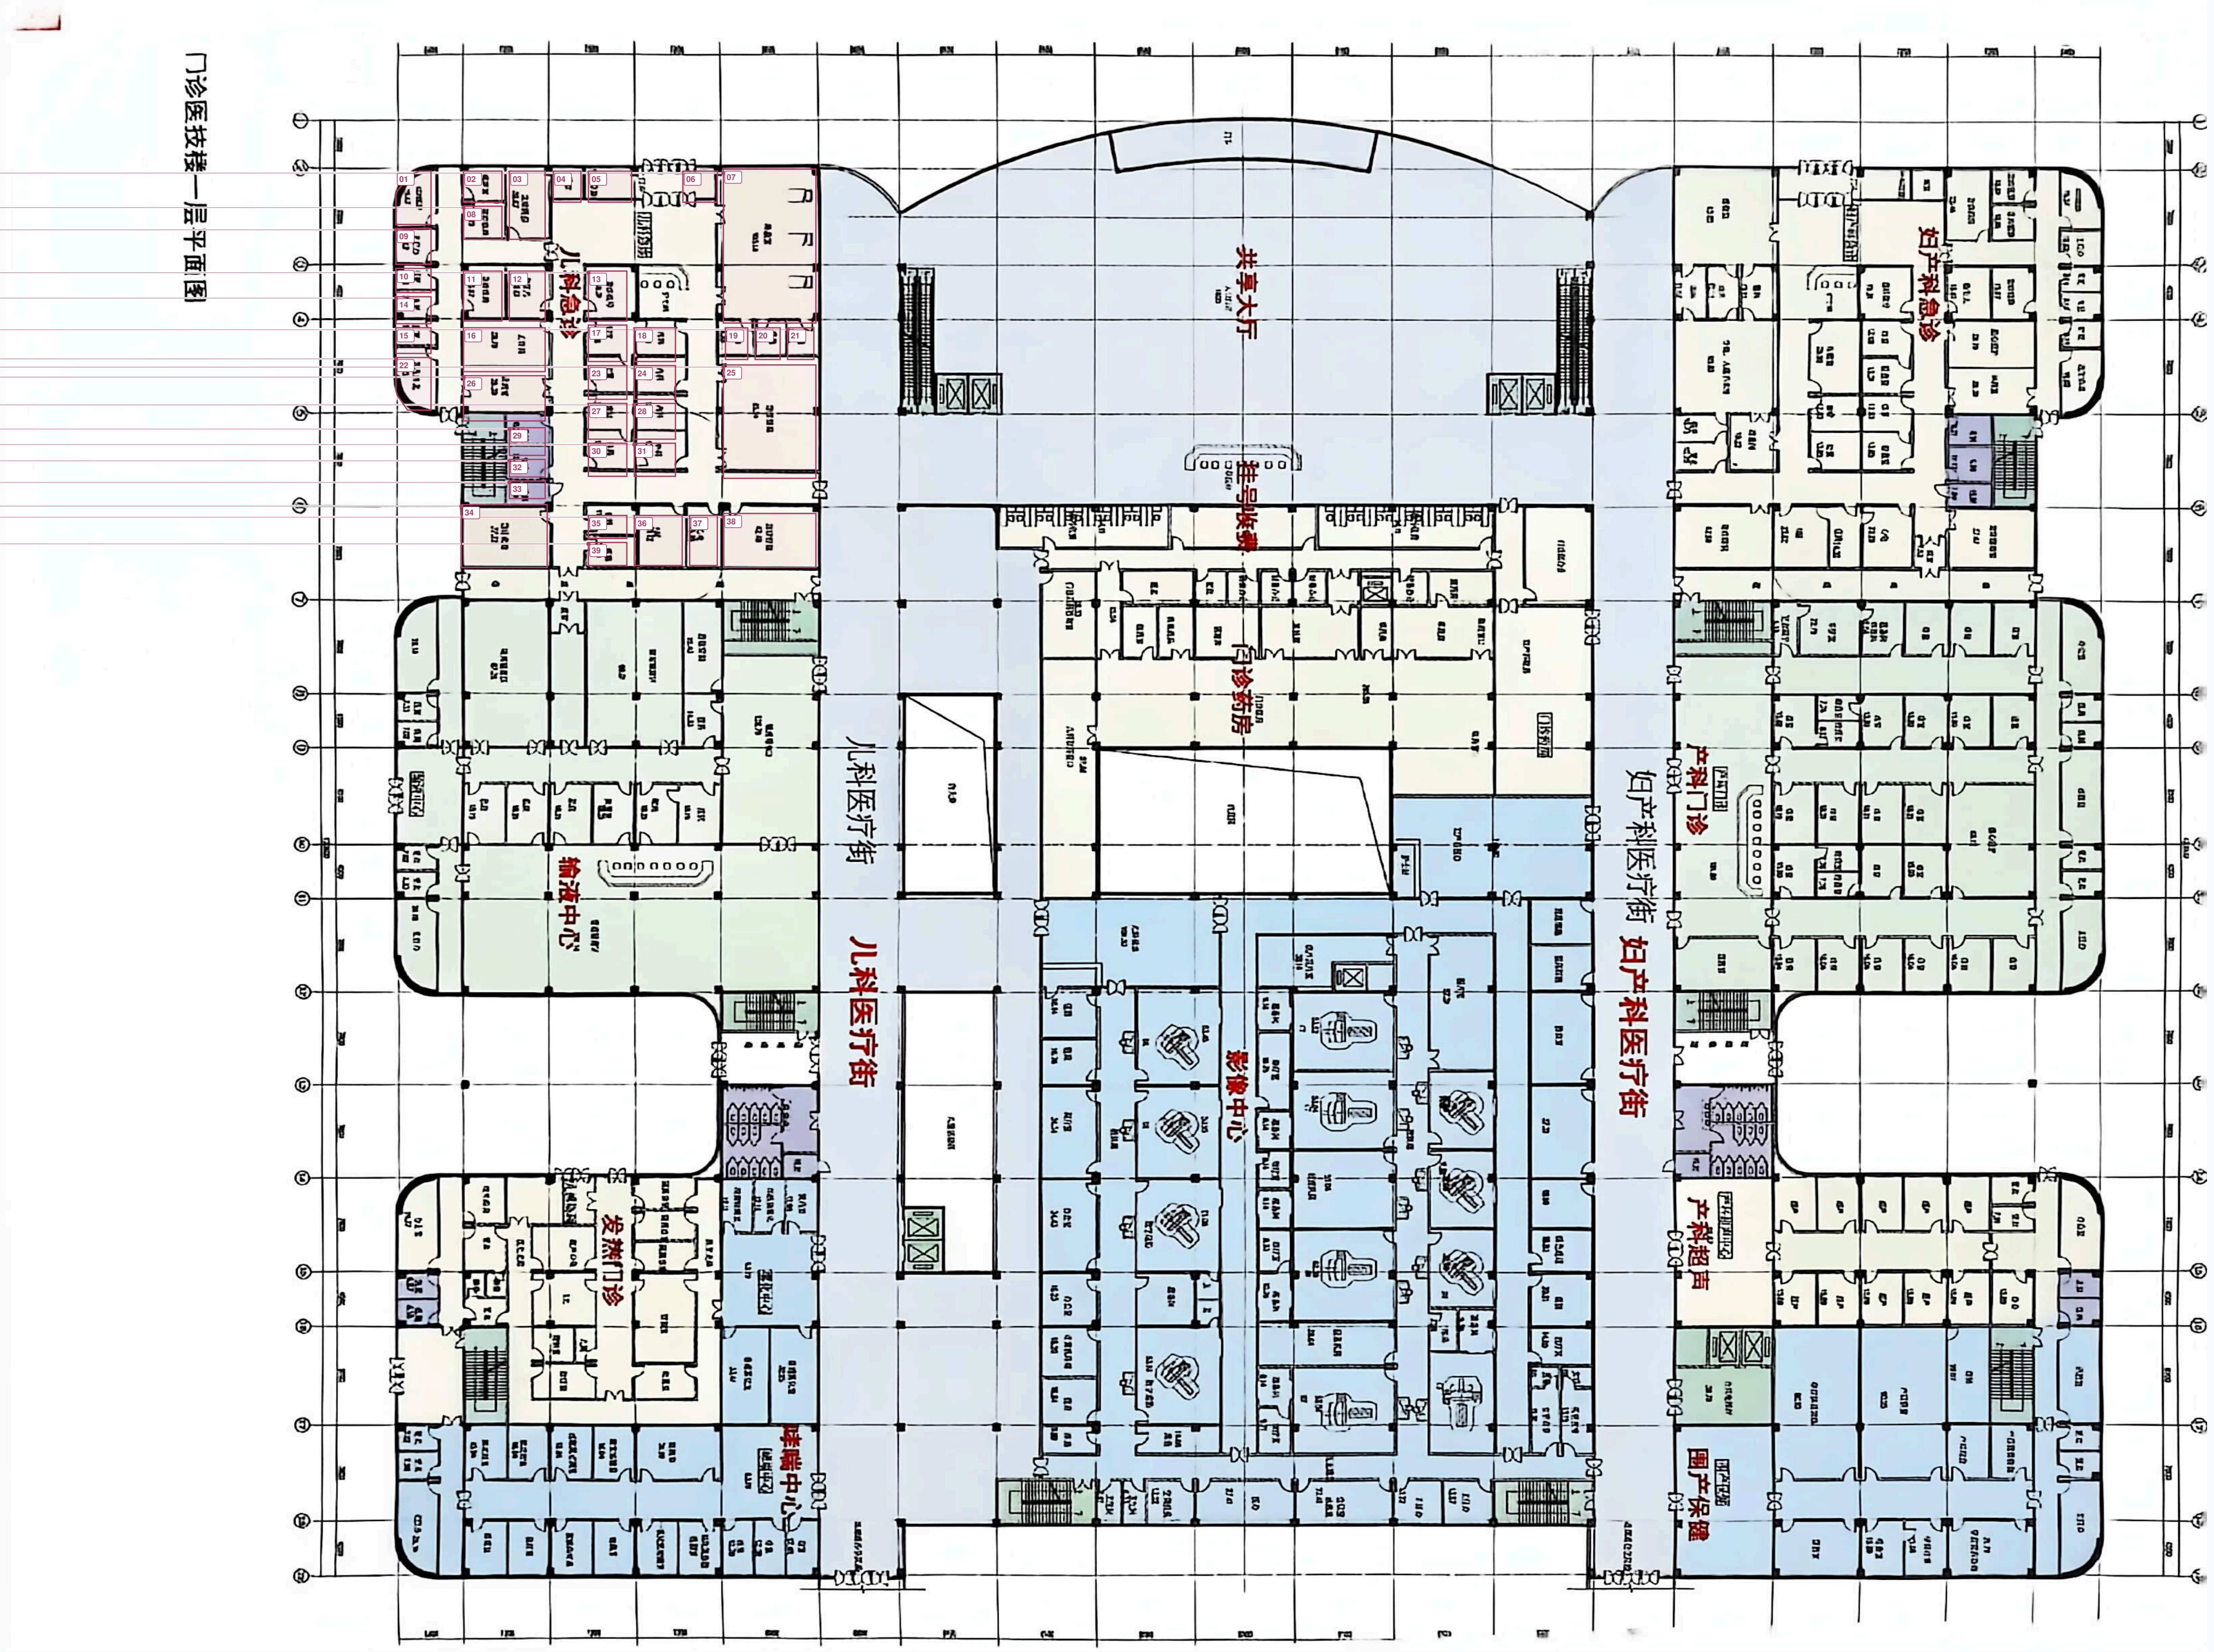

07号平面｜总图**02**_妇产科急诊｜标注草稿：候选均待确认

共 38 项；核对号先左栏后右栏，各栏自上而下；按“01=名称，02=名称”分批回复。

边栏：核对号｜S编号｜候选用途（把握程度）；依据见同目录核对清单。原图未改动。

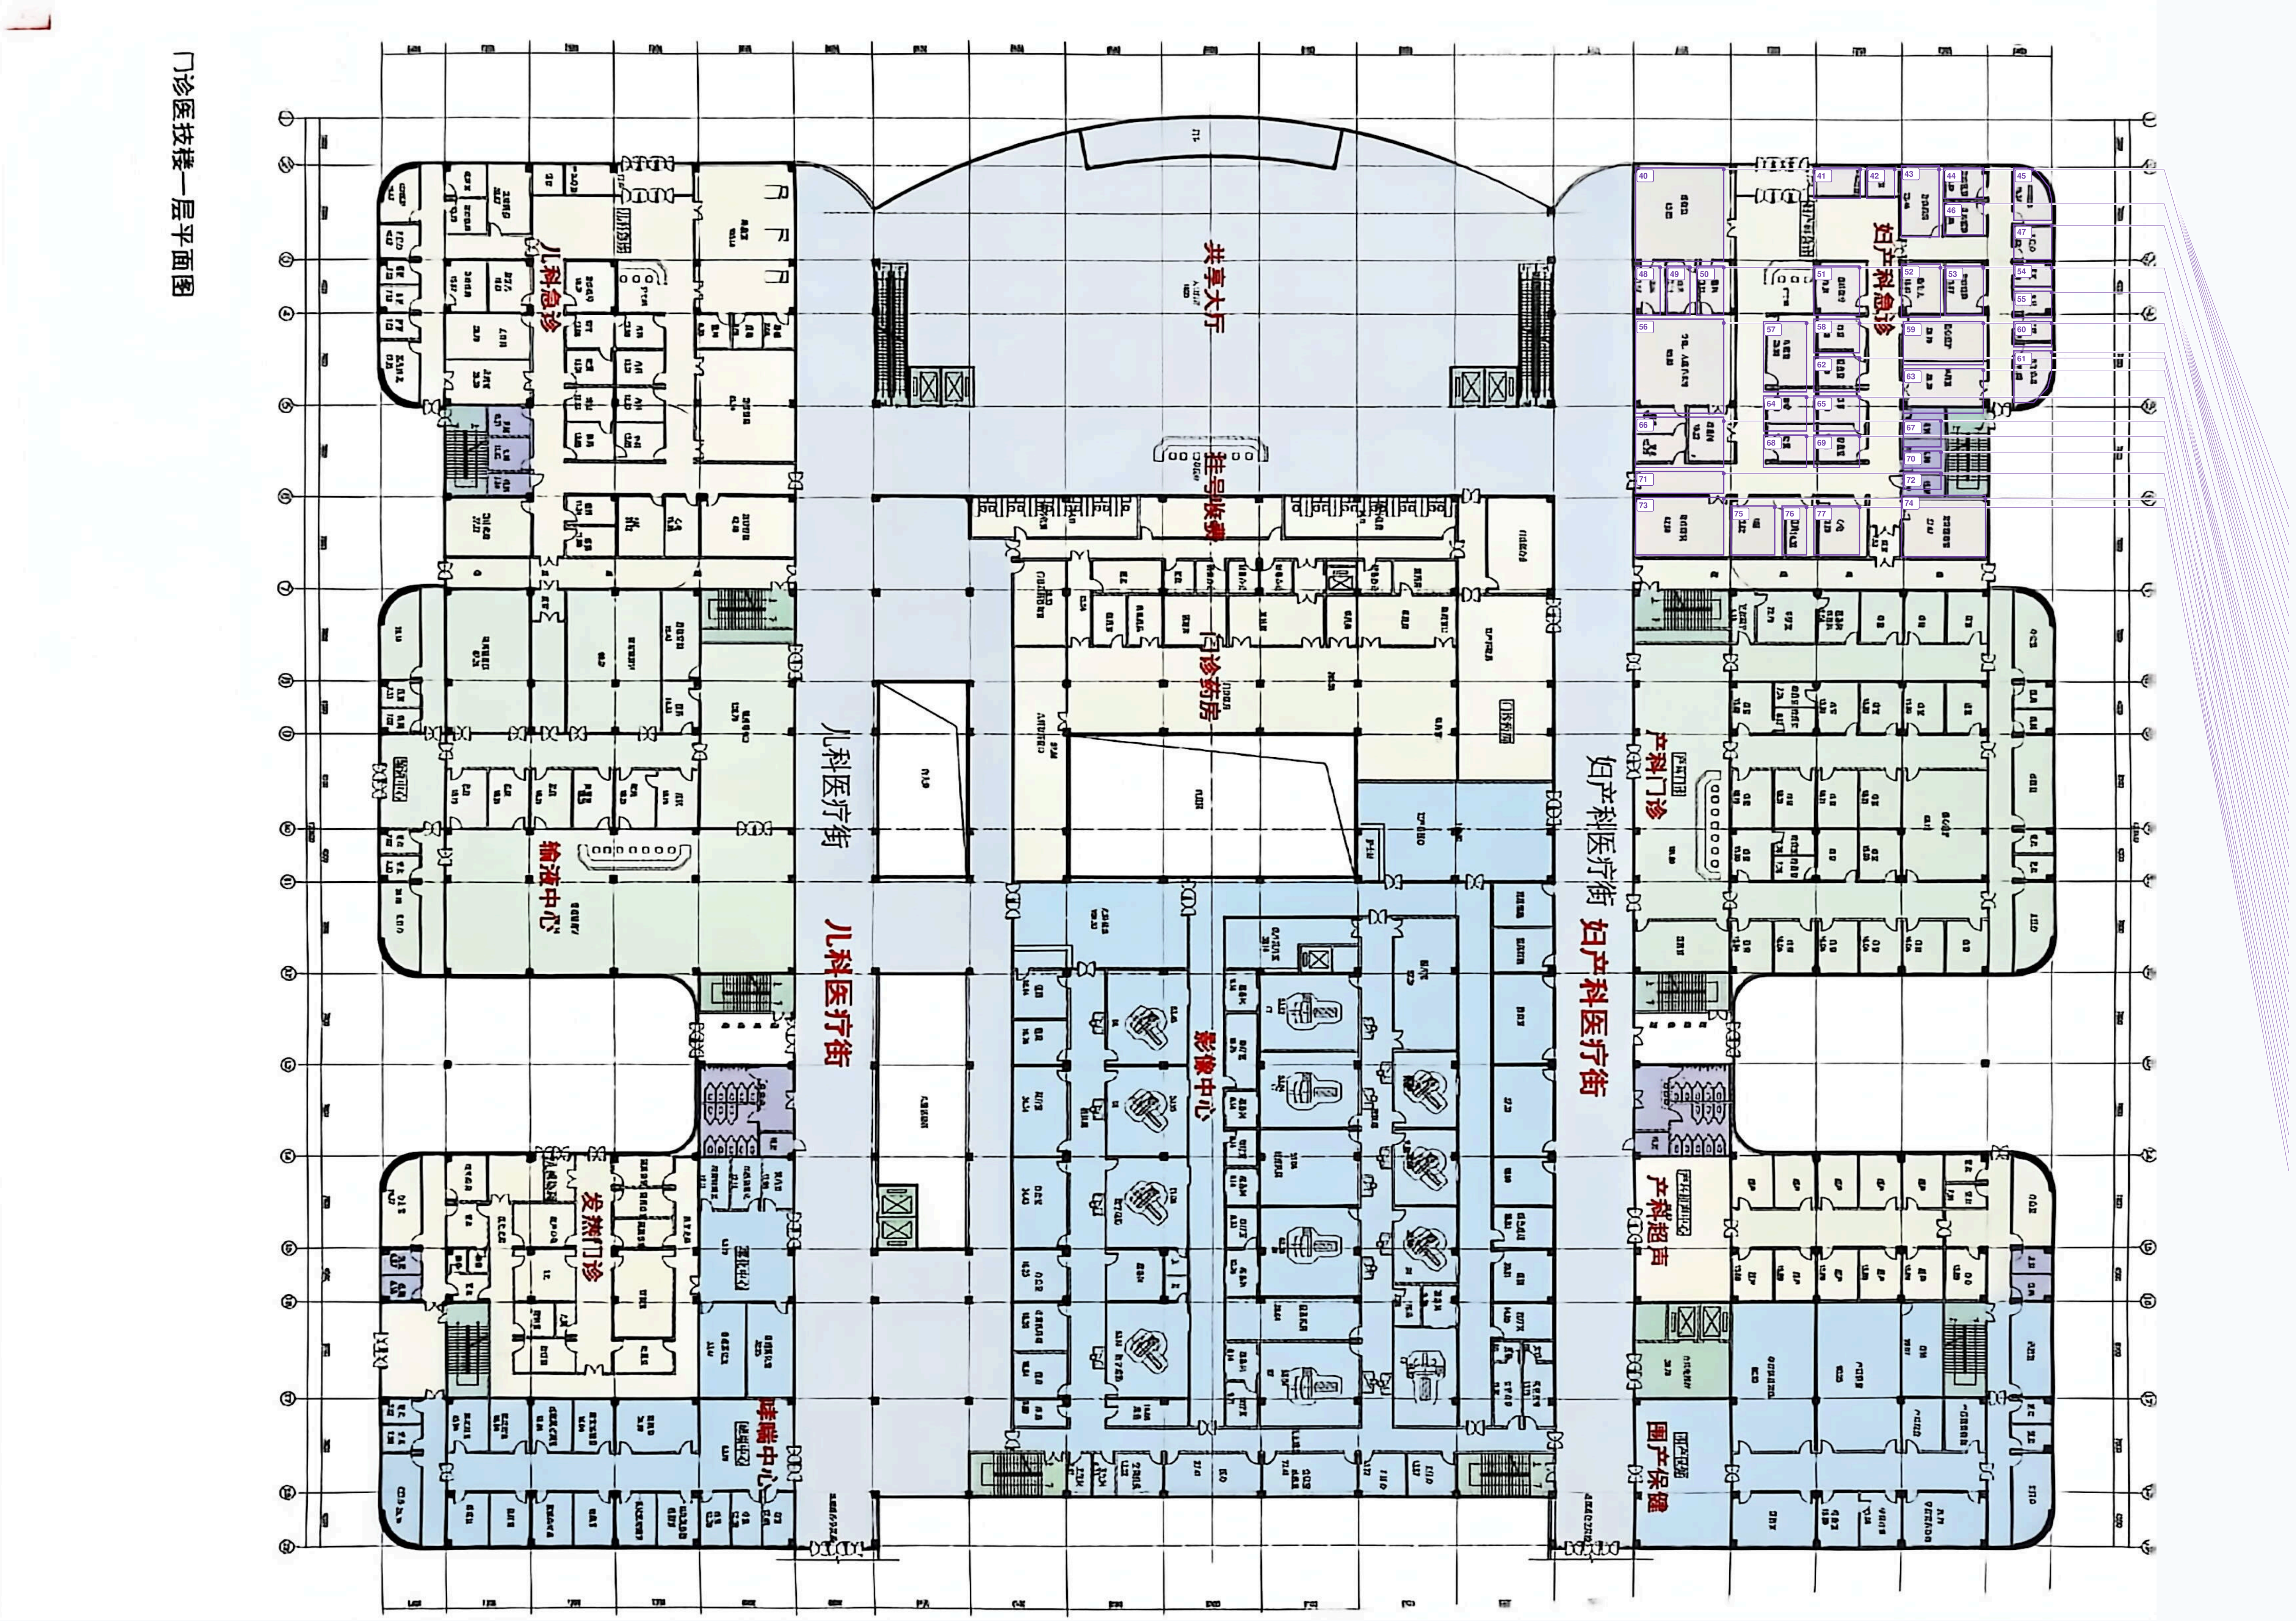

40｜**S052**｜妇产科急诊｜候选：观察室 / 留观室（低）
41｜**S055**｜妇产科急诊｜候选：挂号收费 / 服务用房（低）
42｜**S057**｜妇产科急诊｜候选：设备用房 / 库房（低）
43｜**S059**｜妇产科急诊｜候选：检查室 / 处置室（低）
44｜**S061**｜妇产科急诊｜候选：工作人员支持用房（低）
45｜**S062**｜妇产科急诊｜候选：办公室 / 值班室（低）
46｜**S063**｜妇产科急诊｜候选：工作人员支持用房（低）
47｜**S064**｜妇产科急诊｜候选：库房 / 设备用房（低）
48｜**S065**｜妇产科急诊｜候选：卫生间 / 支持用房（低）
49｜**S066**｜妇产科急诊｜候选：卫生间 / 支持用房（低）
50｜**S067**｜妇产科急诊｜候选：工作人员支持用房（低）
51｜**S069**｜妇产科急诊｜候选：妇产科诊室 / 检查室（低）
52｜**S070**｜妇产科急诊｜候选：**B**超检查室 / 诊室（中）
53｜**S071**｜妇产科急诊｜候选：检查室 / 处置室（低）
54｜**S072**｜妇产科急诊｜候选：卫生间 / 更衣室（低）
55｜**S073**｜妇产科急诊｜候选：卫生间 / 更衣室（低）
56｜**S074**｜妇产科急诊｜候选：急诊治疗室 / 抢救室（低）
57｜**S075**｜妇产科急诊｜候选：处置室 / 治疗室（低）
58｜**S076**｜妇产科急诊｜候选：妇产科诊室 / 检查室（低）
59｜**S077**｜妇产科急诊｜候选：抢救室 / 观察室（低）
60｜**S078**｜妇产科急诊｜候选：库房 / 设备用房（低）
61｜**S080**｜妇产科急诊｜候选：工作人员支持用房（低）
62｜**S079**｜妇产科急诊｜候选：妇产科诊室 / 检查室（低）
63｜**S081**｜妇产科急诊｜候选：抢救室 / 观察室（低）
64｜**S082**｜妇产科急诊｜候选：库房 / 设备用房（低）
65｜**S083**｜妇产科急诊｜候选：妇产科诊室 / 检查室（低）
66｜**S084**｜妇产科急诊｜候选：患者准备 / 支持用房（低）
67｜**S087**｜妇产科急诊｜候选：设备用房 / 库房（低）
68｜**S085**｜妇产科急诊｜候选：采血 / 检验用房（低）
69｜**S086**｜妇产科急诊｜候选：妇产科诊室 / 检查室（低）
70｜**S089**｜妇产科急诊｜候选：卫生间 / 更衣室（低）
71｜**S090**｜妇产科急诊｜候选：通道 / 前室（低）
72｜**S091**｜妇产科急诊｜候选：卫生间 / 更衣室（低）
73｜**S092**｜妇产科急诊｜候选：观察室 / 留观室（低）
74｜**S096**｜妇产科急诊｜候选：留观室 / 治疗室（低）
75｜**S093**｜妇产科急诊｜候选：检查室 / 处置室（低）
76｜**S094**｜妇产科急诊｜候选：工作人员支持用房 / 检查室（低）
77｜**S095**｜妇产科急诊｜候选：心电图室 / 检查室（低）

07号平面｜总图03_输液中心｜标注草稿：候选均待确认

共 17 项；核对号先左栏后右栏，各栏自上而下；按“01=名称，02=名称”分批回复。

边栏：核对号｜S编号｜候选用途（把握程度）；依据见同目录核对清单。原图未改动。

78｜S098｜输液中心｜候选：办公室 / 值班室（低）
79｜S100｜输液中心｜候选：输液治疗区 / 留观区（中）
80｜S103｜输液中心｜候选：输液治疗区 / 特殊输液区（中）
81｜S104｜输液中心｜候选：输液配药 / 准备室（低）
82｜S106｜输液中心｜候选：输液中心留观区 / 输液区（中）
83｜S107｜输液中心｜候选：库房 / 设备用房（低）
84｜S108｜输液中心｜候选：工作人员支持用房（低）
85｜S109｜输液中心｜候选：库房 / 设备用房（低）
86｜S113｜输液中心｜候选：治疗准备 / 工作人员支持用房（低）
87｜S114｜输液中心｜候选：治疗准备 / 工作人员支持用房（低）
88｜S115｜输液中心｜候选：治疗准备 / 工作人员支持用房（低）
89｜S116｜输液中心｜候选：治疗准备 / 工作人员支持用房（低）
90｜S117｜输液中心｜候选：治疗准备 / 工作人员支持用房（低）
91｜S118｜输液中心｜候选：治疗准备 / 工作人员支持用房（低）
92｜S119｜输液中心｜候选：卫生间 / 更衣室（低）
93｜S122｜输液中心｜候选：卫生间 / 更衣室（低）
94｜S123｜输液中心｜候选：工作人员支持用房（低）

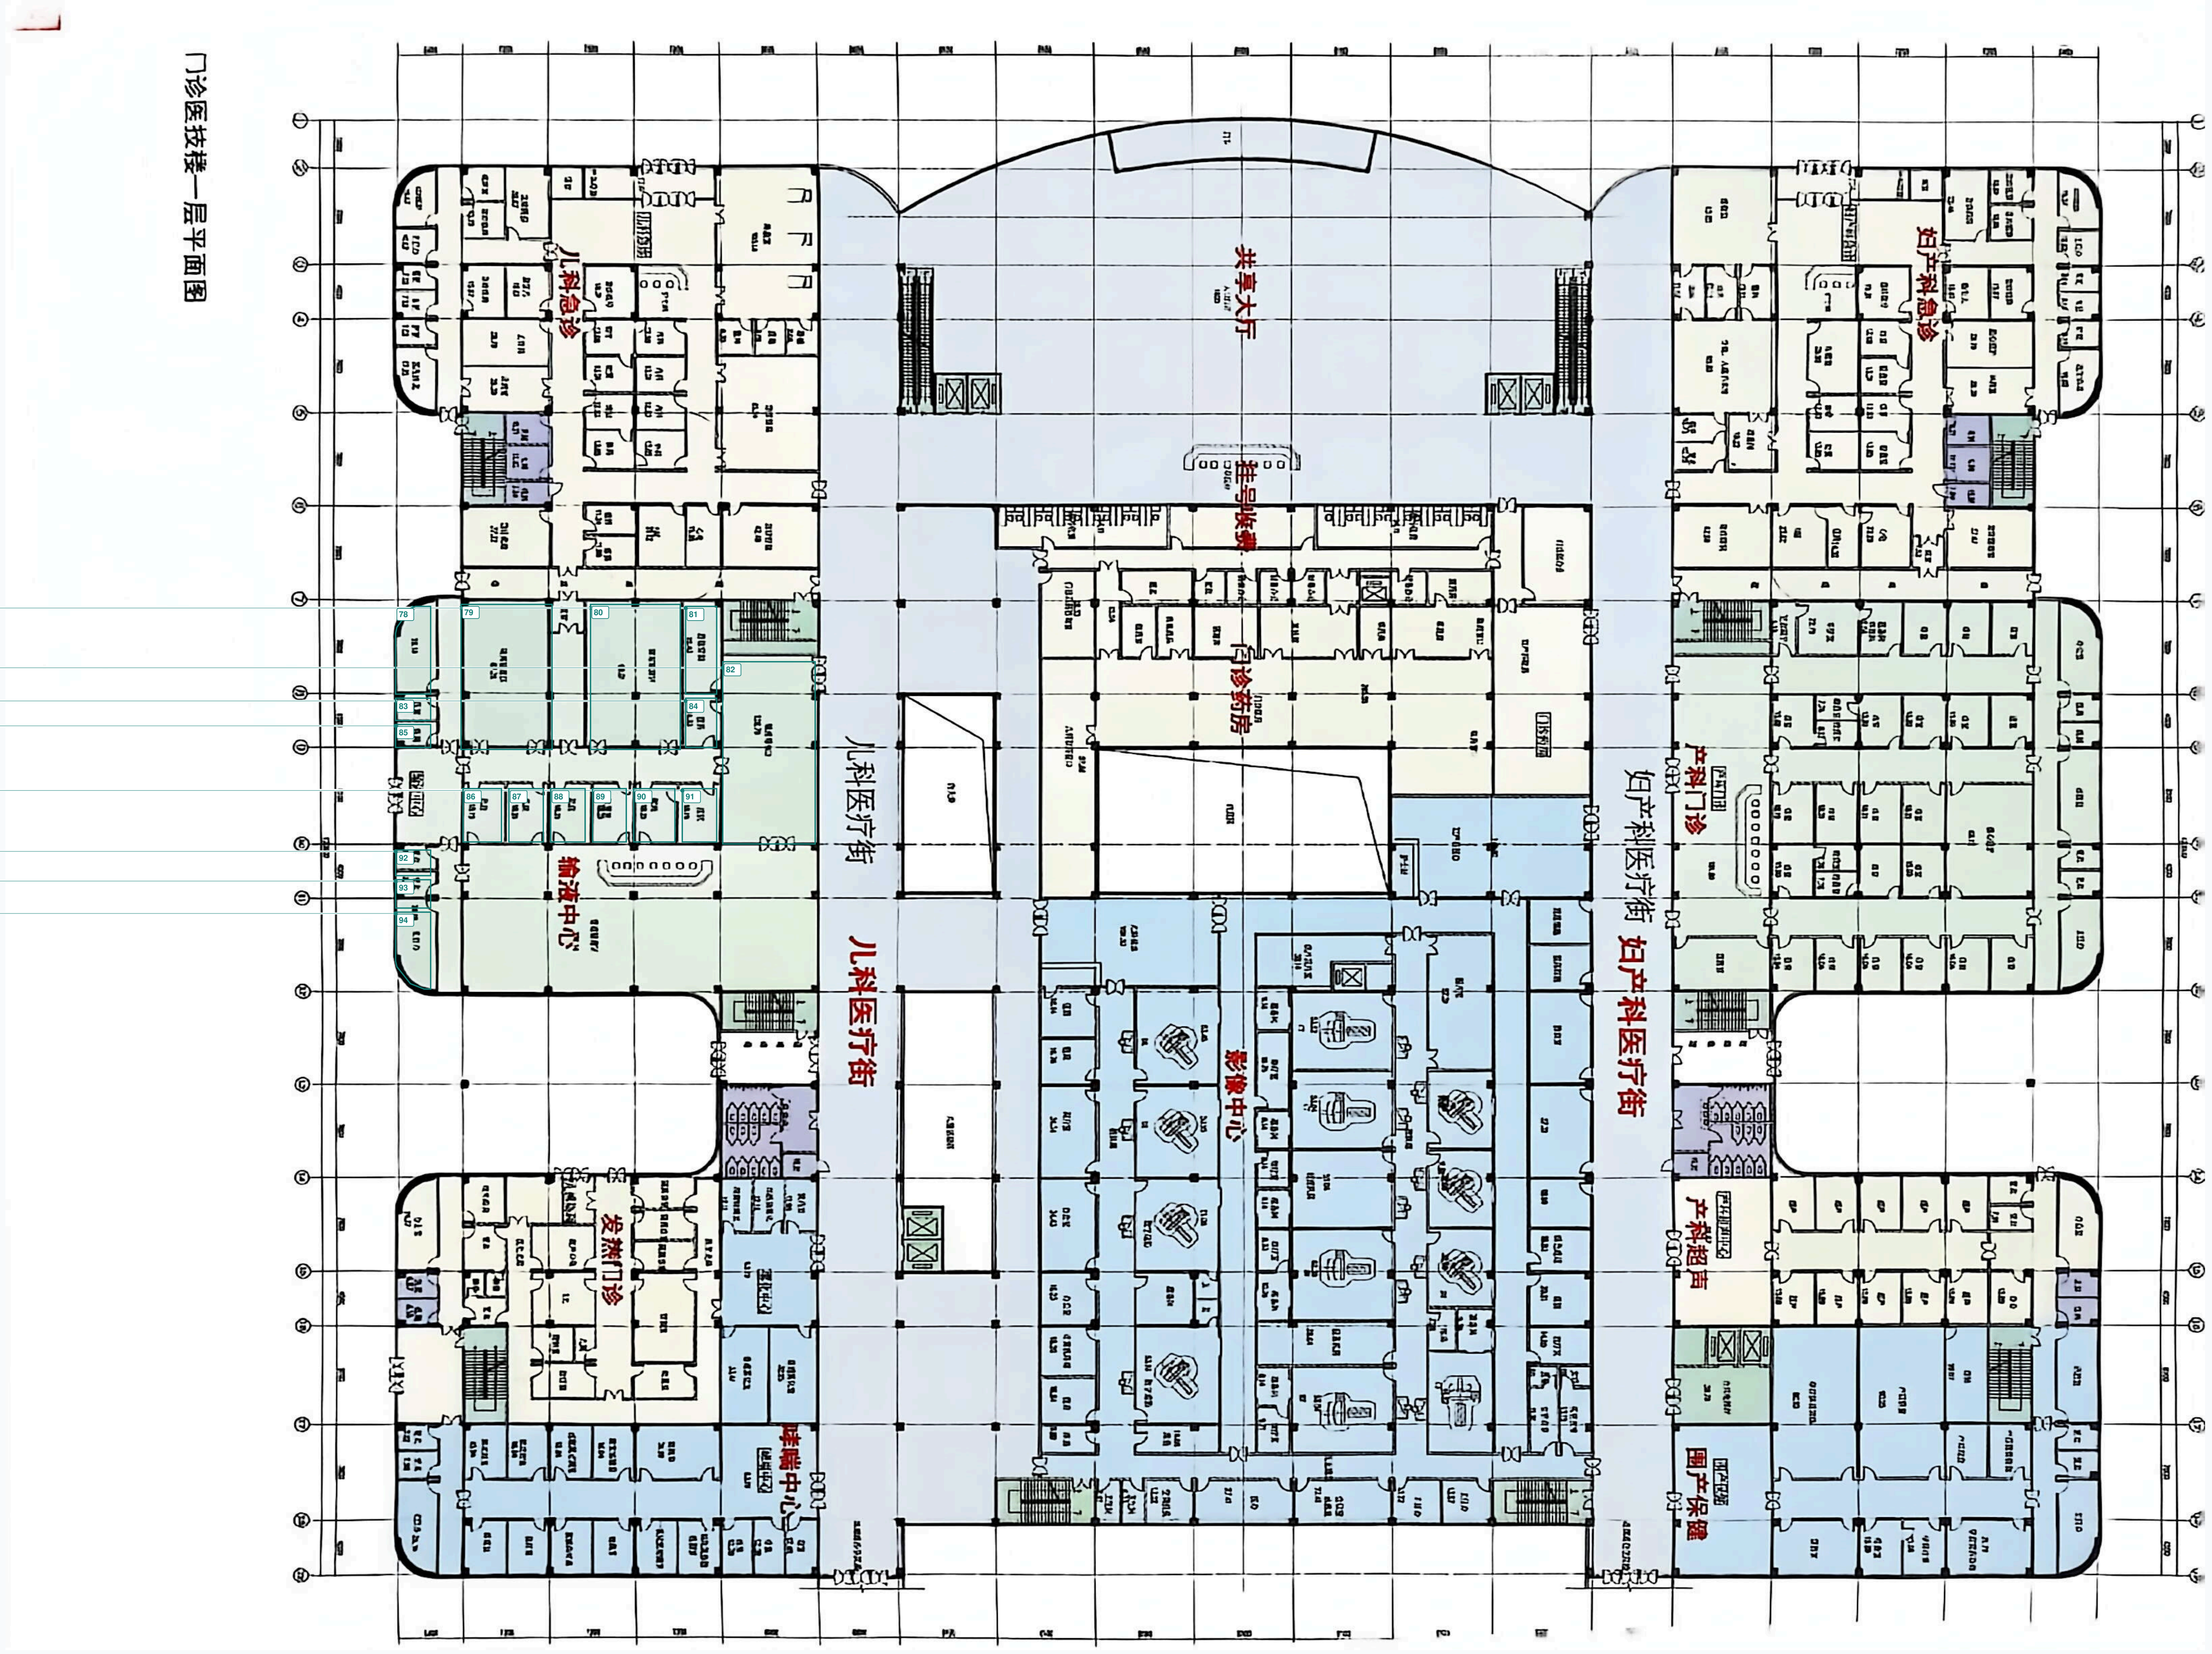

07号平面｜总图04_门诊药房｜标注草稿：候选均待确认

共 21 项；核对号先左栏后右栏，各栏自上而下；按“01=名称，02=名称”分批回复。

边栏：核对号｜S编号｜候选用途（把握程度）；依据见同目录核对清单。原图未改动。

95｜S128｜门诊药房｜候选：门诊服务 / 管理用房（低）
96｜S133｜门诊药房｜候选：药房配套 / 工作人员用房（低）
97｜S134｜门诊药房｜候选：库房 / 设备用房（低）
98｜S135｜门诊药房｜候选：工作人员支持用房（低）
99｜S136｜门诊药房｜候选：工作人员支持用房（低）
100｜S137｜门诊药房｜候选：工作人员支持用房（低）
101｜S138｜门诊药房｜候选：工作人员支持用房（低）
102｜S140｜门诊药房｜候选：设备用房 / 库房（低）
103｜S141｜门诊药房｜候选：工作人员支持用房（低）
104｜S143｜门诊药房｜候选：药房配套 / 工作人员用房（低）
105｜S144｜门诊药房｜候选：药房配套 / 工作人员用房（低）
106｜S145｜门诊药房｜候选：药房配套 / 工作人员用房（低）
107｜S146｜门诊药房｜候选：药房配套 / 工作人员用房（低）
108｜S147｜门诊药房｜候选：药房配套 / 工作人员用房（低）
109｜S148｜门诊药房｜候选：药房配套 / 工作人员用房（低）
110｜S149｜门诊药房｜候选：药房配套 / 工作人员用房（低）
111｜S150｜门诊药房｜候选：药房配套 / 工作人员用房（低）
112｜S151｜门诊药房｜候选：药房配套 / 工作人员用房（低）
113｜S153｜门诊药房｜候选：药房 / 库房（低）
114｜S154｜门诊药房｜候选：药房配套 / 工作人员用房（低）
115｜S155｜门诊药房｜候选：内庭院 / 中庭（是否露天待确认）（中）

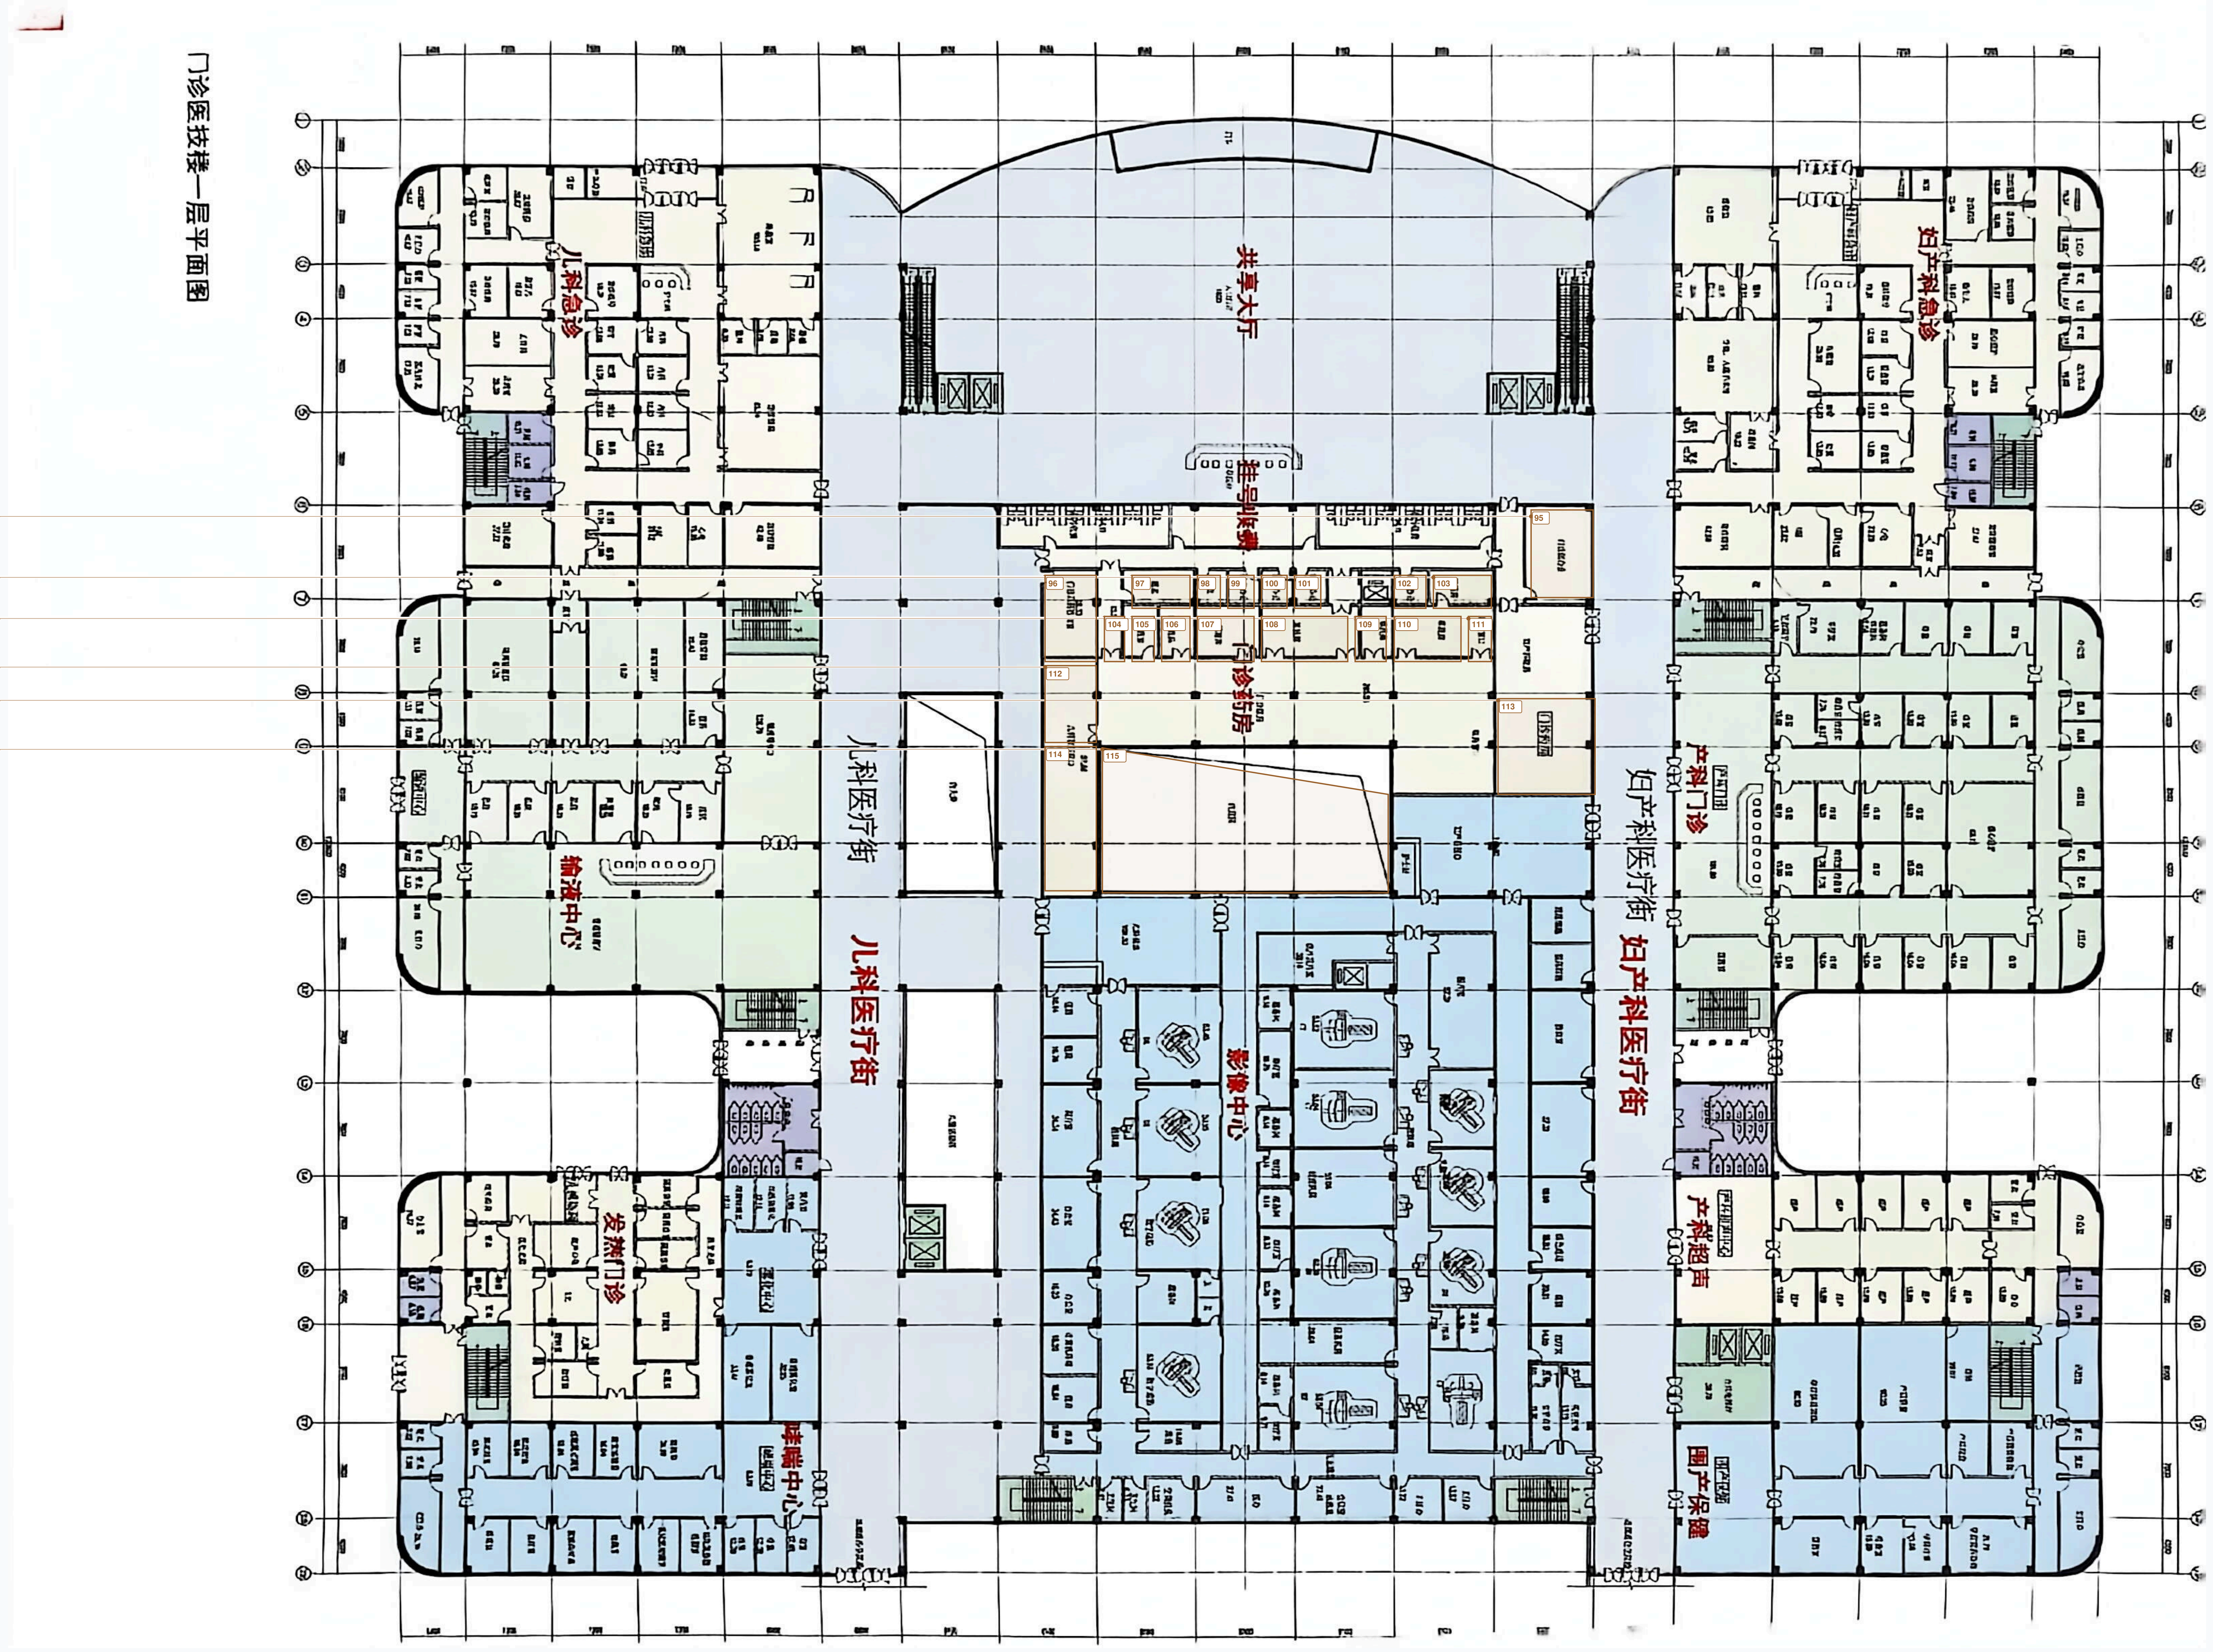

07号平面｜总图05_产科门诊｜标注草稿：候选均待确认

共 37 项；核对号先左栏后右栏，各栏自上而下；按“01=名称，02=名称”分批回复。

边栏：核对号｜S编号｜候选用途（把握程度）；依据见同目录核对清单。原图未改动。

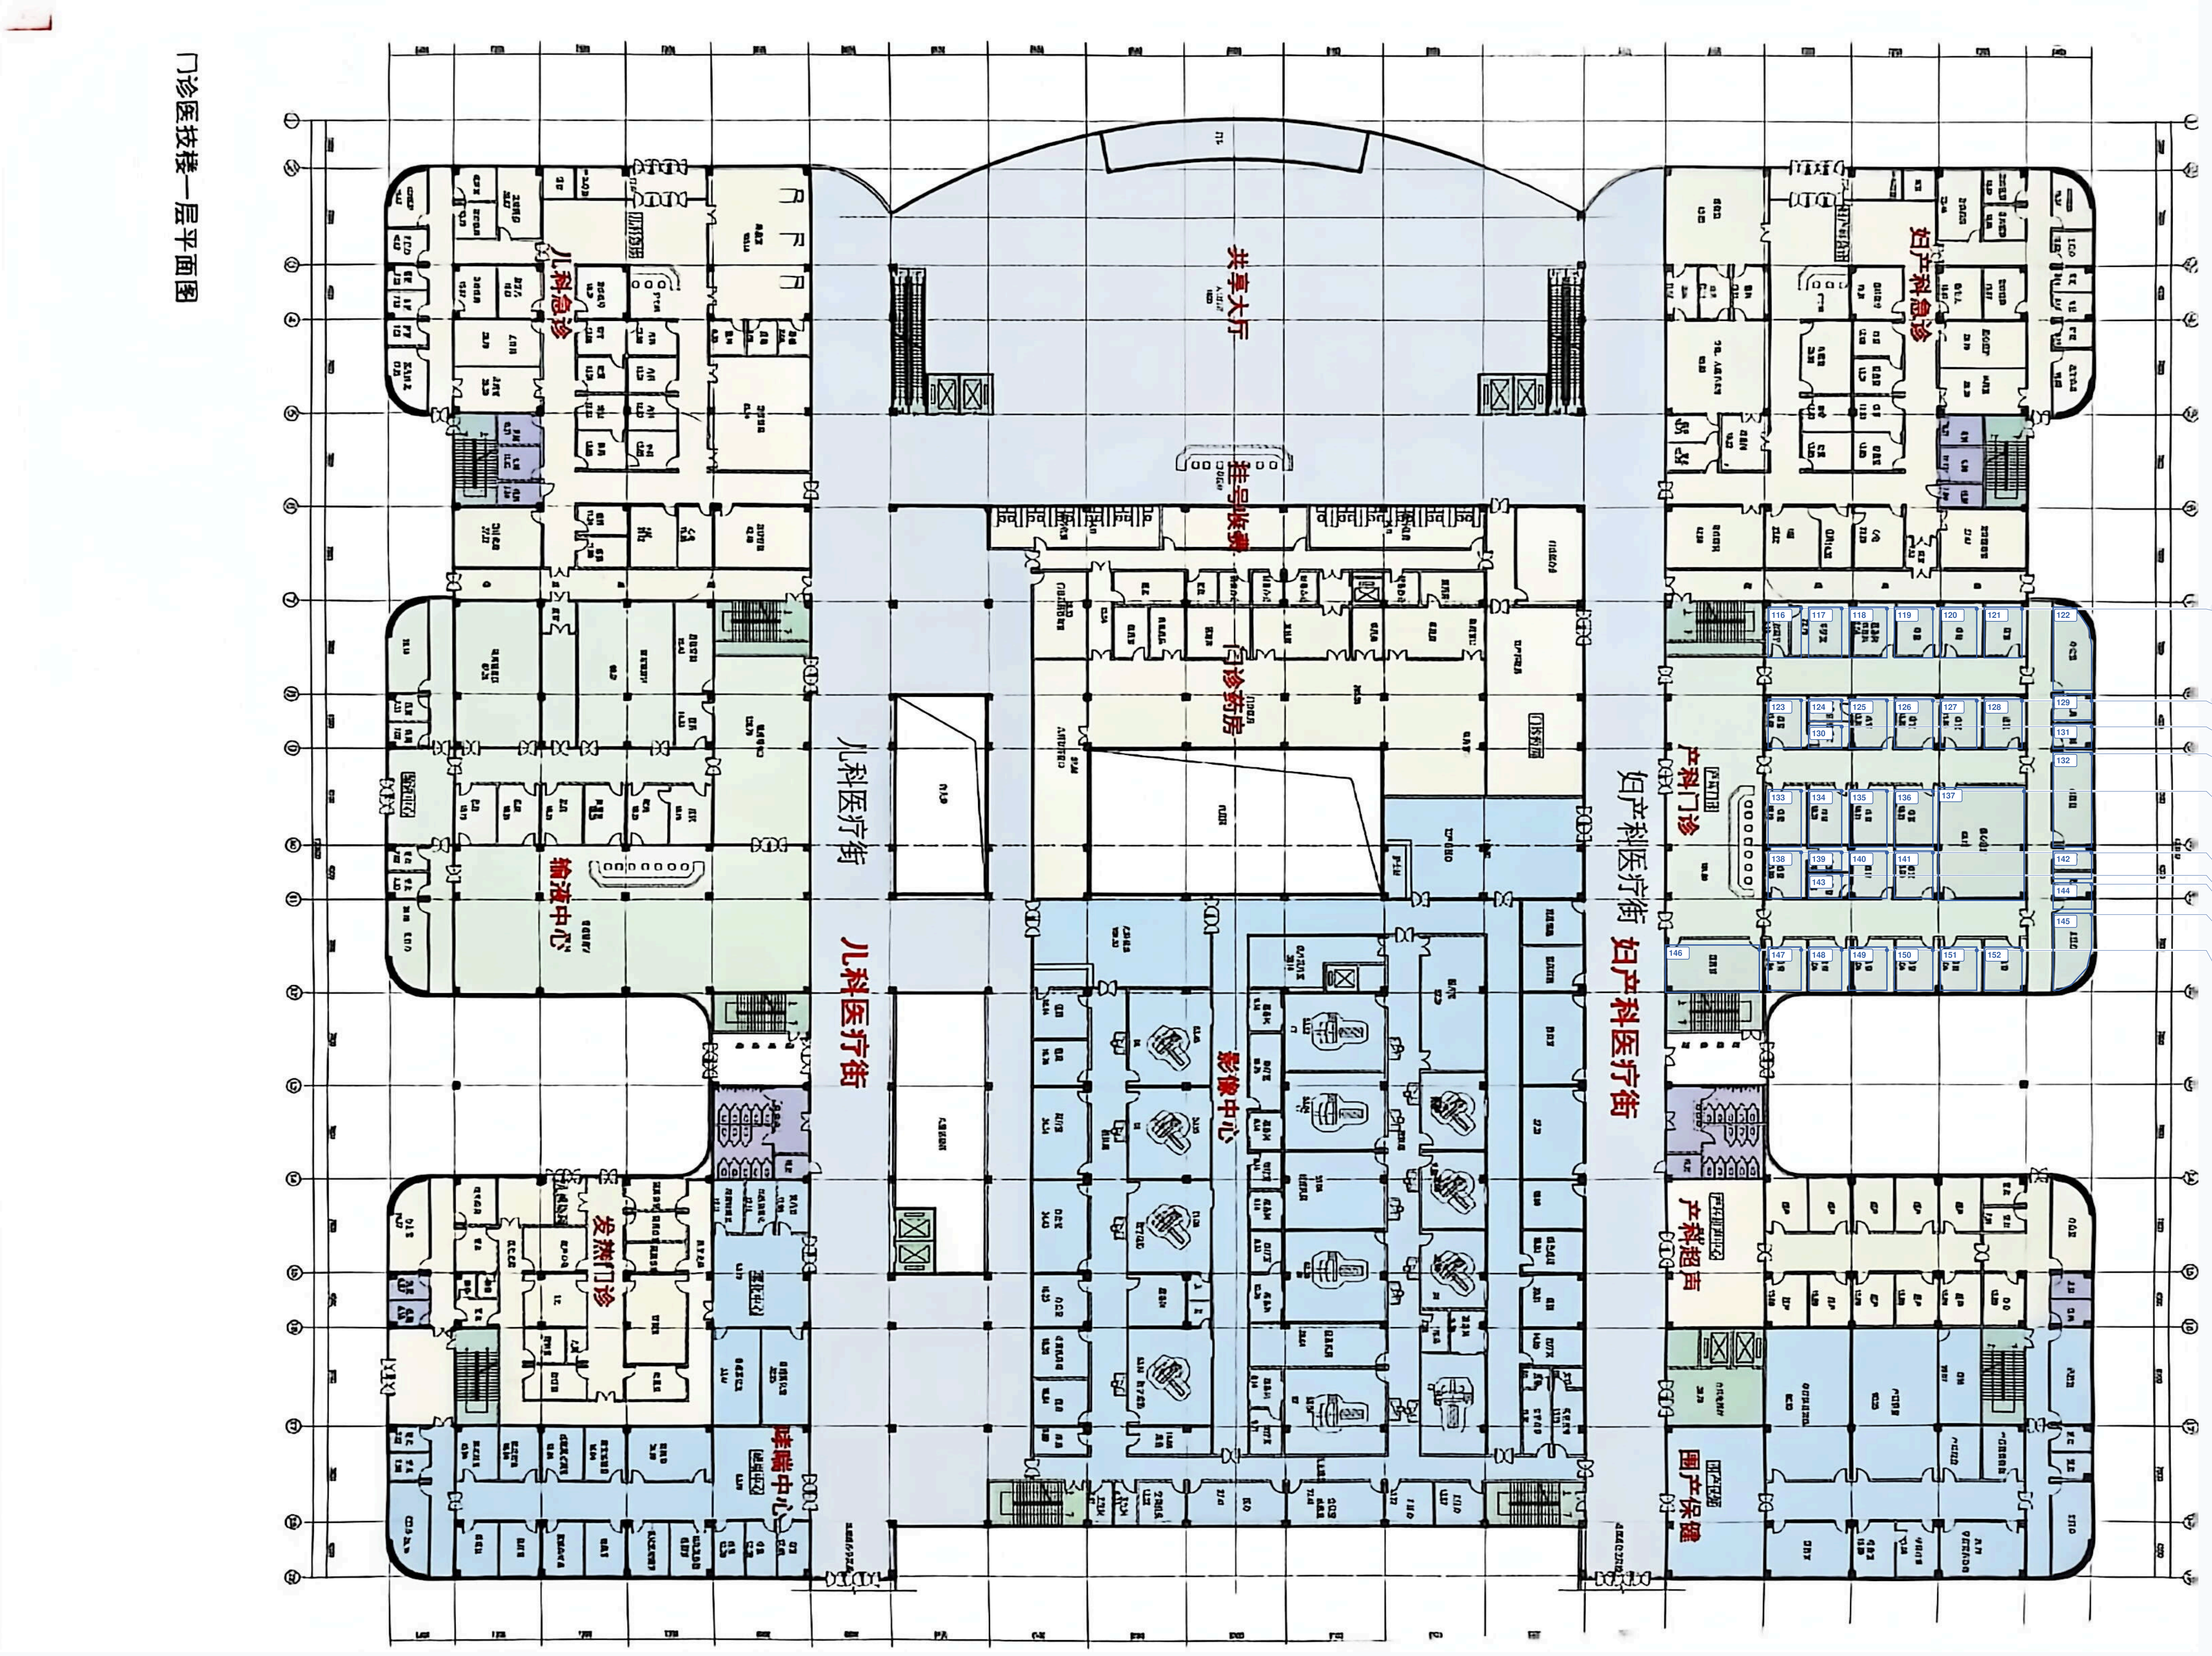

116｜S161｜产科门诊｜候选：产科诊室 / 检查室（低）
117｜S163｜产科门诊｜候选：产科诊室 / 检查室（低）
118｜S165｜产科门诊｜候选：产科诊室 / 检查室（低）
119｜S167｜产科门诊｜候选：产科诊室 / 检查室（低）
120｜S169｜产科门诊｜候选：产科诊室 / 检查室（低）
121｜S171｜产科门诊｜候选：产科诊室 / 检查室（低）
122｜S173｜产科门诊｜候选：办公室 / 值班室（低）
123｜S175｜产科门诊｜候选：产科诊室 / 检查室（低）
124｜S176｜产科门诊｜候选：患者准备 / 支持用房（低）
125｜S177｜产科门诊｜候选：产科诊室 / 检查室（低）
126｜S178｜产科门诊｜候选：产科诊室 / 检查室（低）
127｜S179｜产科门诊｜候选：产科诊室 / 检查室（低）
128｜S180｜产科门诊｜候选：处置室 / 检查室（低）
129｜S181｜产科门诊｜候选：库房 / 设备用房（低）
130｜S182｜产科门诊｜候选：患者准备 / 支持用房（低）
131｜S183｜产科门诊｜候选：库房 / 设备用房（低）
132｜S184｜产科门诊｜候选：工作人员支持用房（低）
133｜S186｜产科门诊｜候选：产科诊室 / 检查室（低）
134｜S187｜产科门诊｜候选：产科诊室 / 检查室（低）
135｜S188｜产科门诊｜候选：产科诊室 / 检查室（低）
136｜S189｜产科门诊｜候选：产科诊室 / 检查室（低）
137｜S190｜产科门诊｜候选：产科检查 / 治疗室（中）
138｜S191｜产科门诊｜候选：产科诊室 / 检查室（低）
139｜S192｜产科门诊｜候选：患者准备 / 支持用房（低）
140｜S193｜产科门诊｜候选：产科诊室 / 检查室（低）
141｜S194｜产科门诊｜候选：产科诊室 / 检查室（低）
142｜S195｜产科门诊｜候选：卫生间 / 更衣室（低）
143｜S196｜产科门诊｜候选：患者准备 / 支持用房（低）
144｜S199｜产科门诊｜候选：卫生间 / 更衣室（低）
145｜S200｜产科门诊｜候选：办公室 / 值班室（低）
146｜S201｜产科门诊｜候选：宣教室 / 诊室（低）
147｜S202｜产科门诊｜候选：产科诊室 / 检查室（低）
148｜S203｜产科门诊｜候选：产科诊室 / 检查室（低）
149｜S204｜产科门诊｜候选：产科诊室 / 检查室（低）
150｜S205｜产科门诊｜候选：产科诊室 / 检查室（低）
151｜S206｜产科门诊｜候选：产科诊室 / 检查室（低）
152｜S207｜产科门诊｜候选：产科诊室 / 检查室（低）

07号平面｜总图06_发热门诊与哮喘中心｜标注草稿：候选均待确认

共 40 项；核对号先左栏后右栏，各栏自上而下；按“01=名称，02=名称”分批回复。

边栏：核对号｜S编号｜候选用途（把握程度）；依据见同目录核对清单。原图未改动。

153｜S211｜发热门诊与哮喘中心｜候选：办公室 / 值班室（低）
154｜S213｜发热门诊与哮喘中心｜候选：工作人员支持用房（低）
155｜S217｜发热门诊与哮喘中心｜候选：护士站 / 服务工作区（低）
156｜S220｜发热门诊与哮喘中心｜候选：发热诊室 / 检查室（低）
157｜S223｜发热门诊与哮喘中心｜候选：呼吸功能检查 / 治疗室（低）
158｜S225｜发热门诊与哮喘中心｜候选：哮喘治疗 / 检查室（低）
159｜S227｜发热门诊与哮喘中心｜候选：哮喘诊室 / 检查室（低）
160｜S229｜发热门诊与哮喘中心｜候选：卫生间 / 支持用房（低）
161｜S230｜发热门诊与哮喘中心｜候选：发热诊室 / 检查室（低）
162｜S231｜发热门诊与哮喘中心｜候选：发热诊室 / 检查室（低）
163｜S232｜发热门诊与哮喘中心｜候选：卫生间 / 更衣室（低）
164｜S233｜发热门诊与哮喘中心｜候选：患者准备 / 支持用房（低）
165｜S234｜发热门诊与哮喘中心｜候选：检验室 / 处置室（低）
166｜S235｜发热门诊与哮喘中心｜候选：隔离观察 / 治疗室（低）
167｜S236｜发热门诊与哮喘中心｜候选：卫生间 / 更衣室（低）
168｜S237｜发热门诊与哮喘中心｜候选：卫生间 / 支持用房（低）
169｜S238｜发热门诊与哮喘中心｜候选：门斗 / 入口区（低）
170｜S240｜发热门诊与哮喘中心｜候选：工作人员支持用房（低）
171｜S241｜发热门诊与哮喘中心｜候选：患者准备 / 支持用房（低）
172｜S242｜发热门诊与哮喘中心｜候选：哮喘治疗 / 检查室（低）
173｜S243｜发热门诊与哮喘中心｜候选：呼吸功能检查 / 治疗室（低）
174｜S244｜发热门诊与哮喘中心｜候选：工作人员支持用房（低）
175｜S245｜发热门诊与哮喘中心｜候选：发热诊室 / 检查室（低）
176｜S247｜发热门诊与哮喘中心｜候选：库房 / 设备用房（低）
177｜S248｜发热门诊与哮喘中心｜候选：诊室 / 检查室（低）
178｜S249｜发热门诊与哮喘中心｜候选：诊室 / 检查室（低）
179｜S250｜发热门诊与哮喘中心｜候选：诊室 / 检查室（低）
180｜S251｜发热门诊与哮喘中心｜候选：诊室 / 检查室（低）
181｜S252｜发热门诊与哮喘中心｜候选：诊室 / 检查室（低）
182｜S254｜发热门诊与哮喘中心｜候选：库房 / 设备用房（低）
183｜S255｜发热门诊与哮喘中心｜候选：工作人员支持用房（低）
184｜S258｜发热门诊与哮喘中心｜候选：诊室 / 检查室（低）
185｜S259｜发热门诊与哮喘中心｜候选：诊室 / 检查室（低）
186｜S260｜发热门诊与哮喘中心｜候选：诊室 / 检查室（低）
187｜S261｜发热门诊与哮喘中心｜候选：诊室 / 检查室（低）
188｜S262｜发热门诊与哮喘中心｜候选：诊室 / 检查室（低）
189｜S263｜发热门诊与哮喘中心｜候选：诊室 / 检查室（低）
190｜S264｜发热门诊与哮喘中心｜候选：哮喘诊室 / 检查室（低）
191｜S265｜发热门诊与哮喘中心｜候选：哮喘诊室 / 检查室（低）
192｜S266｜发热门诊与哮喘中心｜候选：哮喘诊室 / 检查室（低）

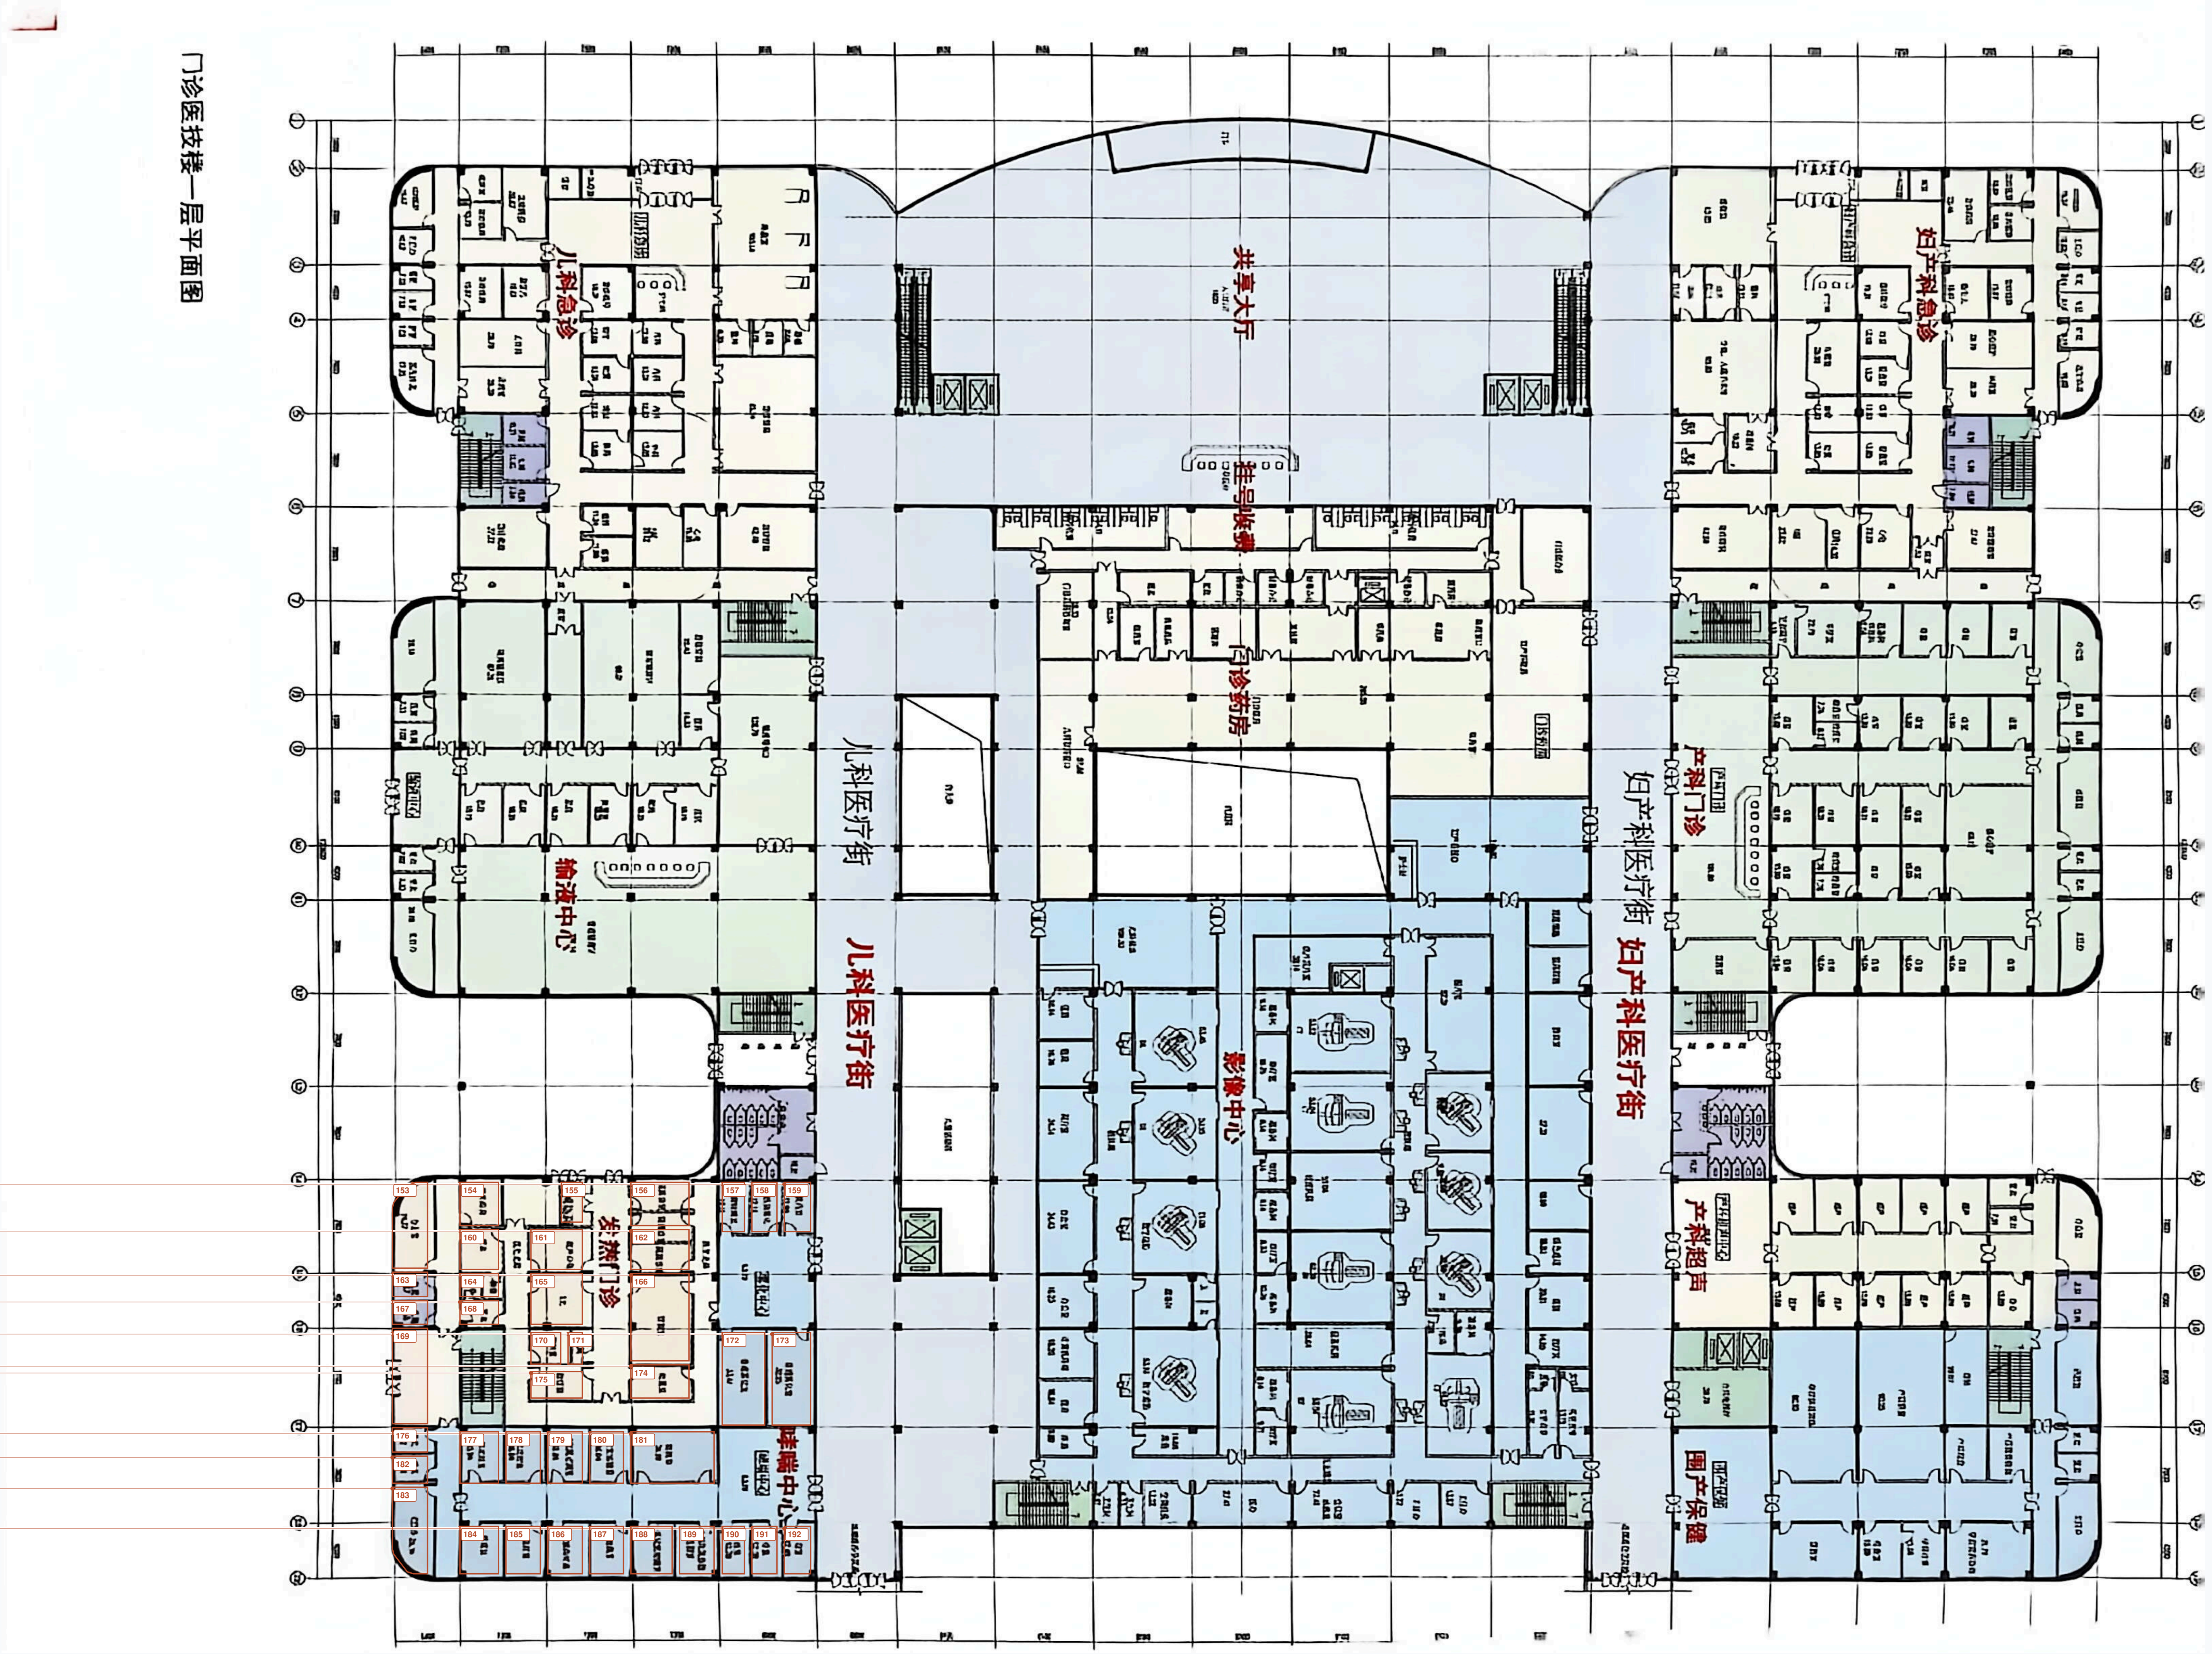

07号平面｜总图07_影像中心｜标注草稿：候选均待确认

共 46 项；核对号先左栏后右栏，各栏自上而下；按“01=名称，02=名称”分批回复。

边栏：核对号｜S编号｜候选用途（把握程度）；依据见同目录核对清单。原图未改动。

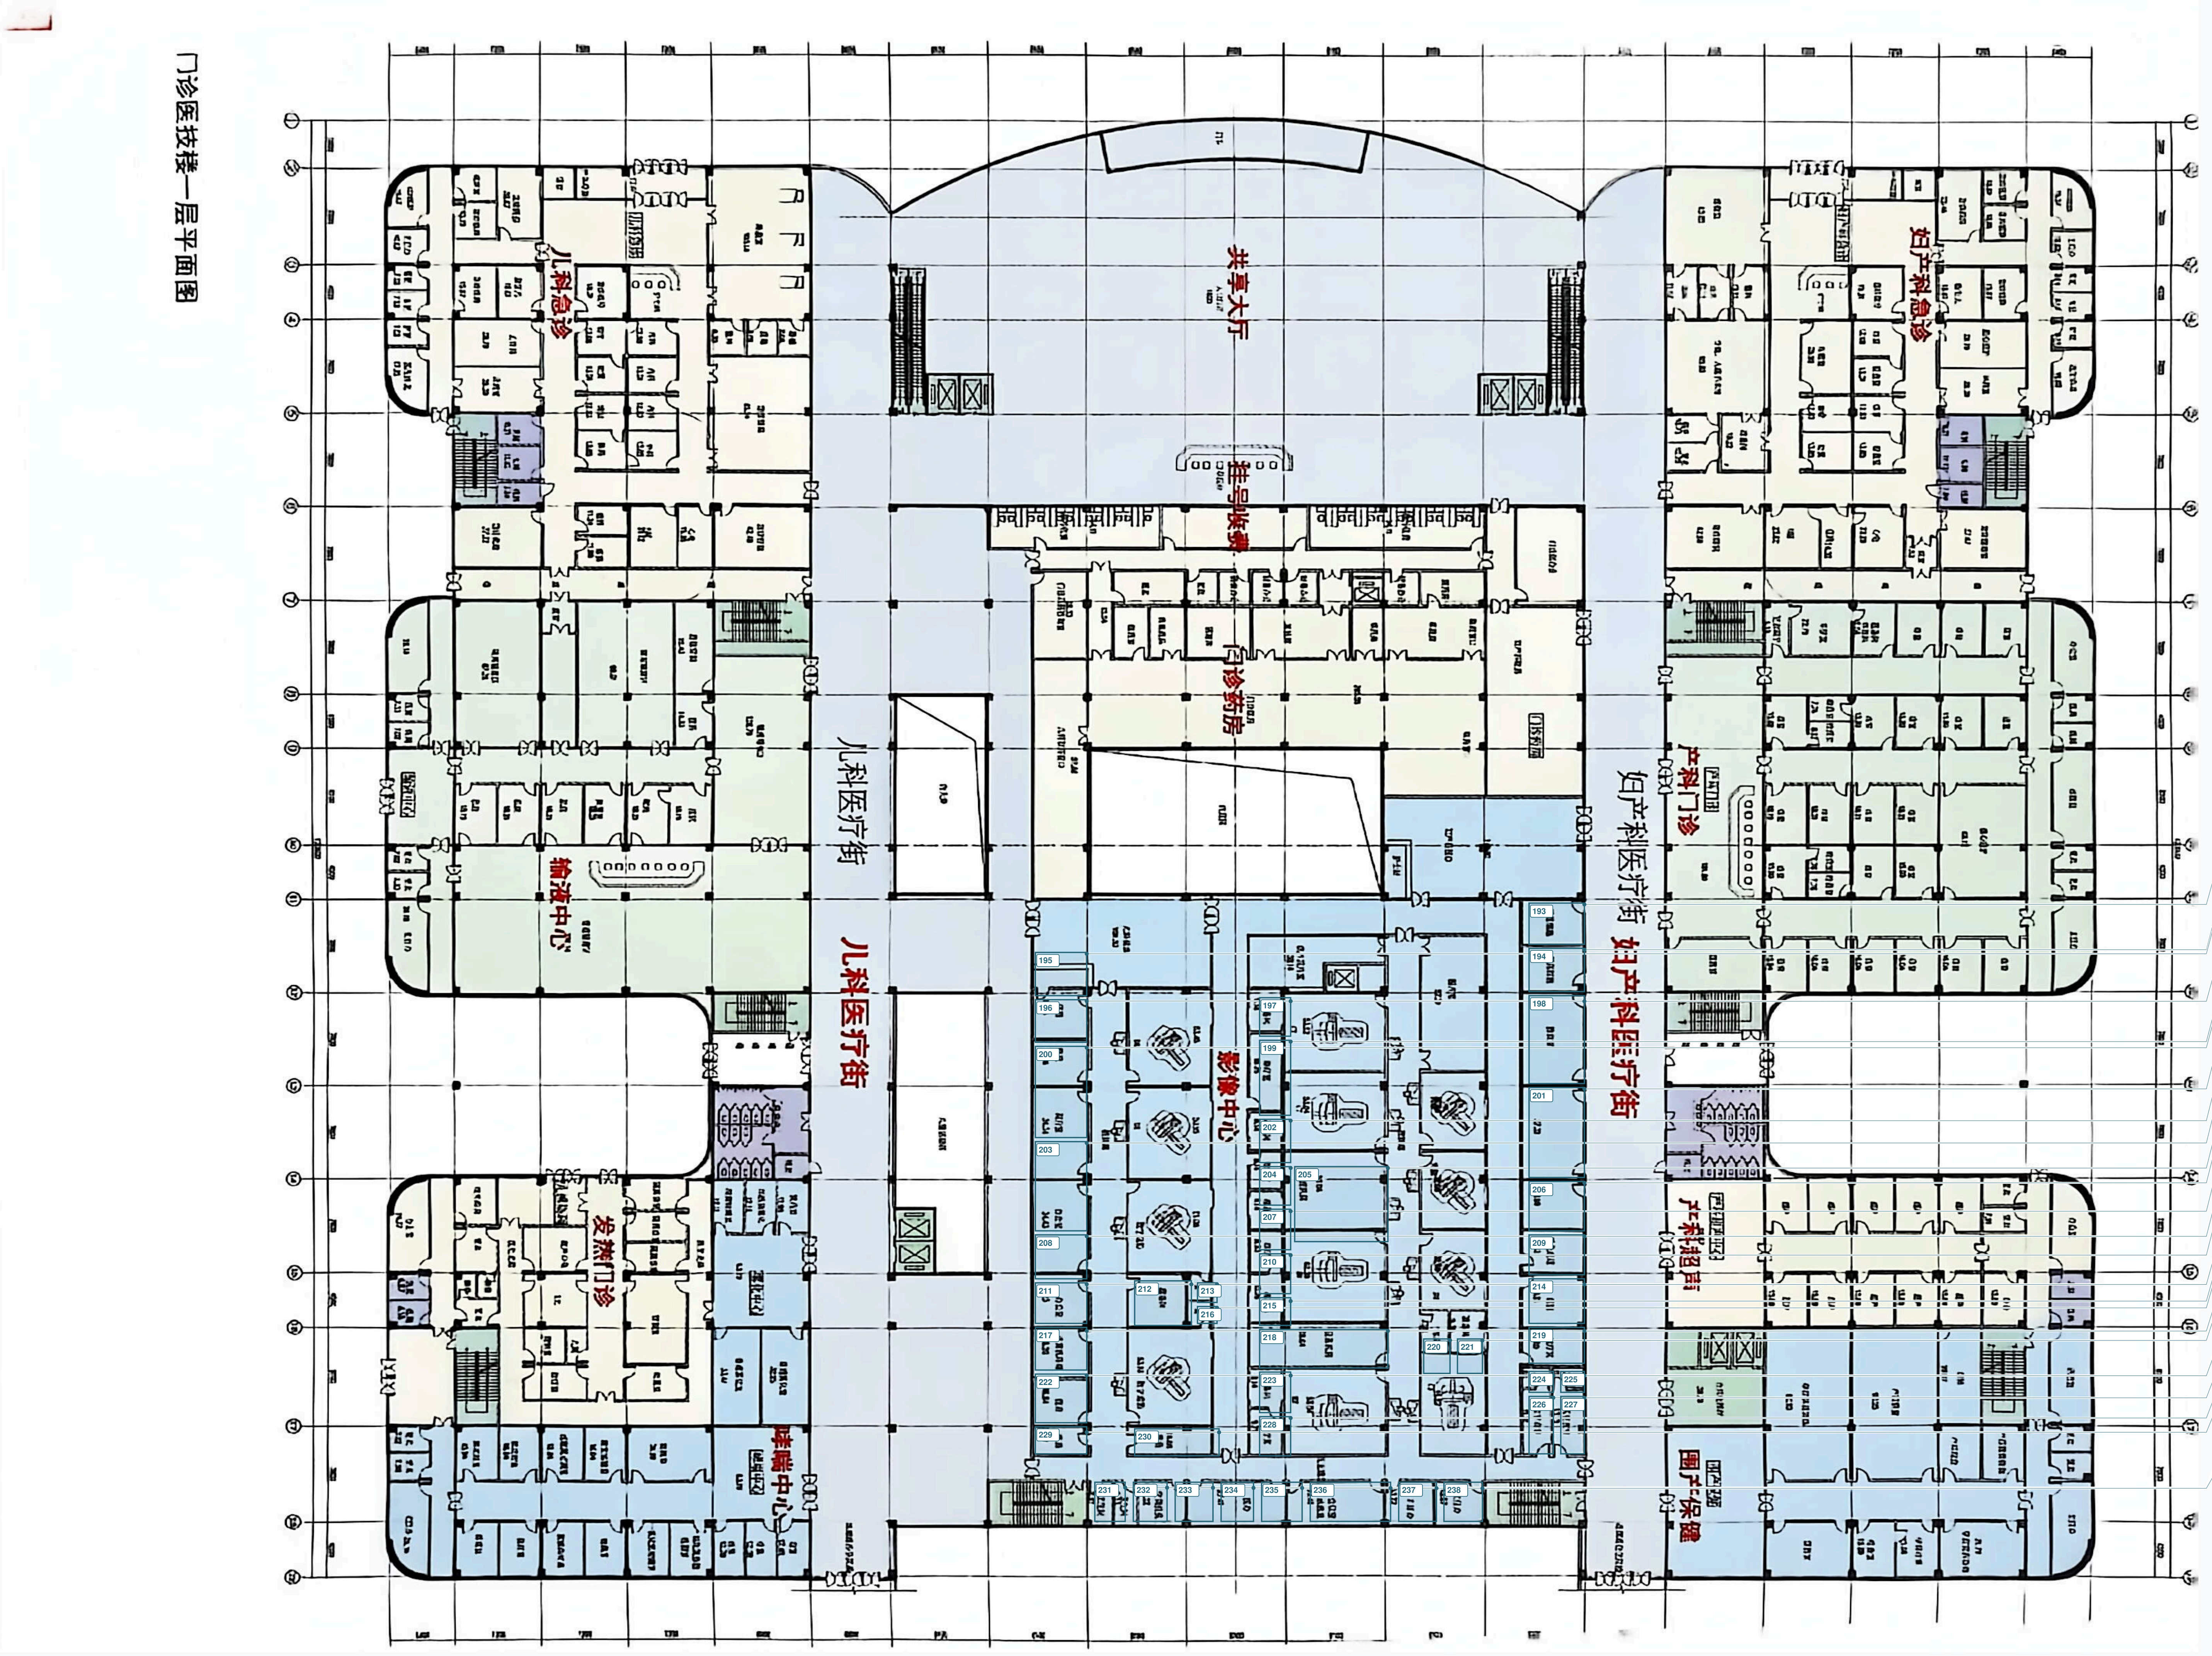

193｜S277｜影像中心｜候选：影像配套用房（低）
194｜S281｜影像中心｜候选：影像配套用房（低）
195｜S278｜影像中心｜候选：影像配套／工作人员用房（低）
196｜S282｜影像中心｜候选：影像配套／工作人员用房（低）
197｜S285｜影像中心｜候选：控制室／检查配套用房（中）
198｜S287｜影像中心｜候选：影像配套用房（低）
199｜S288｜影像中心｜候选：控制室／检查配套用房（中）
200｜S289｜影像中心｜候选：影像配套／工作人员用房（低）
201｜S293｜影像中心｜候选：影像配套用房（低）
202｜S294｜影像中心｜候选：控制室／检查配套用房（中）
203｜S295｜影像中心｜候选：影像配套／工作人员用房（低）
204｜S296｜影像中心｜候选：控制室／检查配套用房（中）
205｜S297｜影像中心｜候选：影像设备／检查准备室（中）
206｜S300｜影像中心｜候选：影像配套用房（低）
207｜S301｜影像中心｜候选：控制室／检查配套用房（中）
208｜S302｜影像中心｜候选：影像配套／工作人员用房（低）
209｜S306｜影像中心｜候选：影像配套用房（低）
210｜S303｜影像中心｜候选：控制室／检查配套用房（中）
211｜S307｜影像中心｜候选：影像配套／工作人员用房（低）
212｜S308｜影像中心｜候选：影像配套／设备机房（中）
213｜S309｜影像中心｜候选：卫生间／患者准备用房（低）
214｜S310｜影像中心｜候选：影像配套用房（低）
215｜S312｜影像中心｜候选：控制室／检查配套用房（中）
216｜S311｜影像中心｜候选：卫生间／患者准备用房（低）
217｜S313｜影像中心｜候选：影像配套／工作人员用房（低）
218｜S315｜影像中心｜候选：设备机房／检查准备室（中）
219｜S316｜影像中心｜候选：影像配套用房（低）
220｜S317｜影像中心｜候选：影像配套用房（低）
221｜S318｜影像中心｜候选：影像配套用房（低）
222｜S319｜影像中心｜候选：影像配套／工作人员用房（低）
223｜S320｜影像中心｜候选：控制室／检查配套用房（中）
224｜S323｜影像中心｜候选：影像配套用房（低）
225｜S324｜影像中心｜候选：影像配套用房（低）
226｜S326｜影像中心｜候选：影像配套用房（低）
227｜S327｜影像中心｜候选：影像配套用房（低）
228｜S325｜影像中心｜候选：控制室／检查配套用房（中）
229｜S328｜影像中心｜候选：影像配套／工作人员用房（低）
230｜S329｜影像中心｜候选：设备机房／检查配套用房（中）
231｜S335｜影像中心｜候选：影像配套／工作人员用房（低）
232｜S336｜影像中心｜候选：影像配套／工作人员用房（低）
233｜S337｜影像中心｜候选：影像配套／工作人员用房（低）
234｜S338｜影像中心｜候选：影像配套／工作人员用房（低）
235｜S339｜影像中心｜候选：影像配套／工作人员用房（低）
236｜S340｜影像中心｜候选：影像配套／工作人员用房（低）
237｜S341｜影像中心｜候选：影像配套／工作人员用房（低）
238｜S342｜影像中心｜候选：影像配套／工作人员用房（低）

07号平面｜总图08_产科超声与围产保健｜标注草稿：候选均待确认

共 29 项；核对号先左栏后右栏，各栏自上而下；按“01=名称，02=名称”分批回复。

边栏：核对号｜S编号｜候选用途（把握程度）；依据见同目录核对清单。原图未改动。

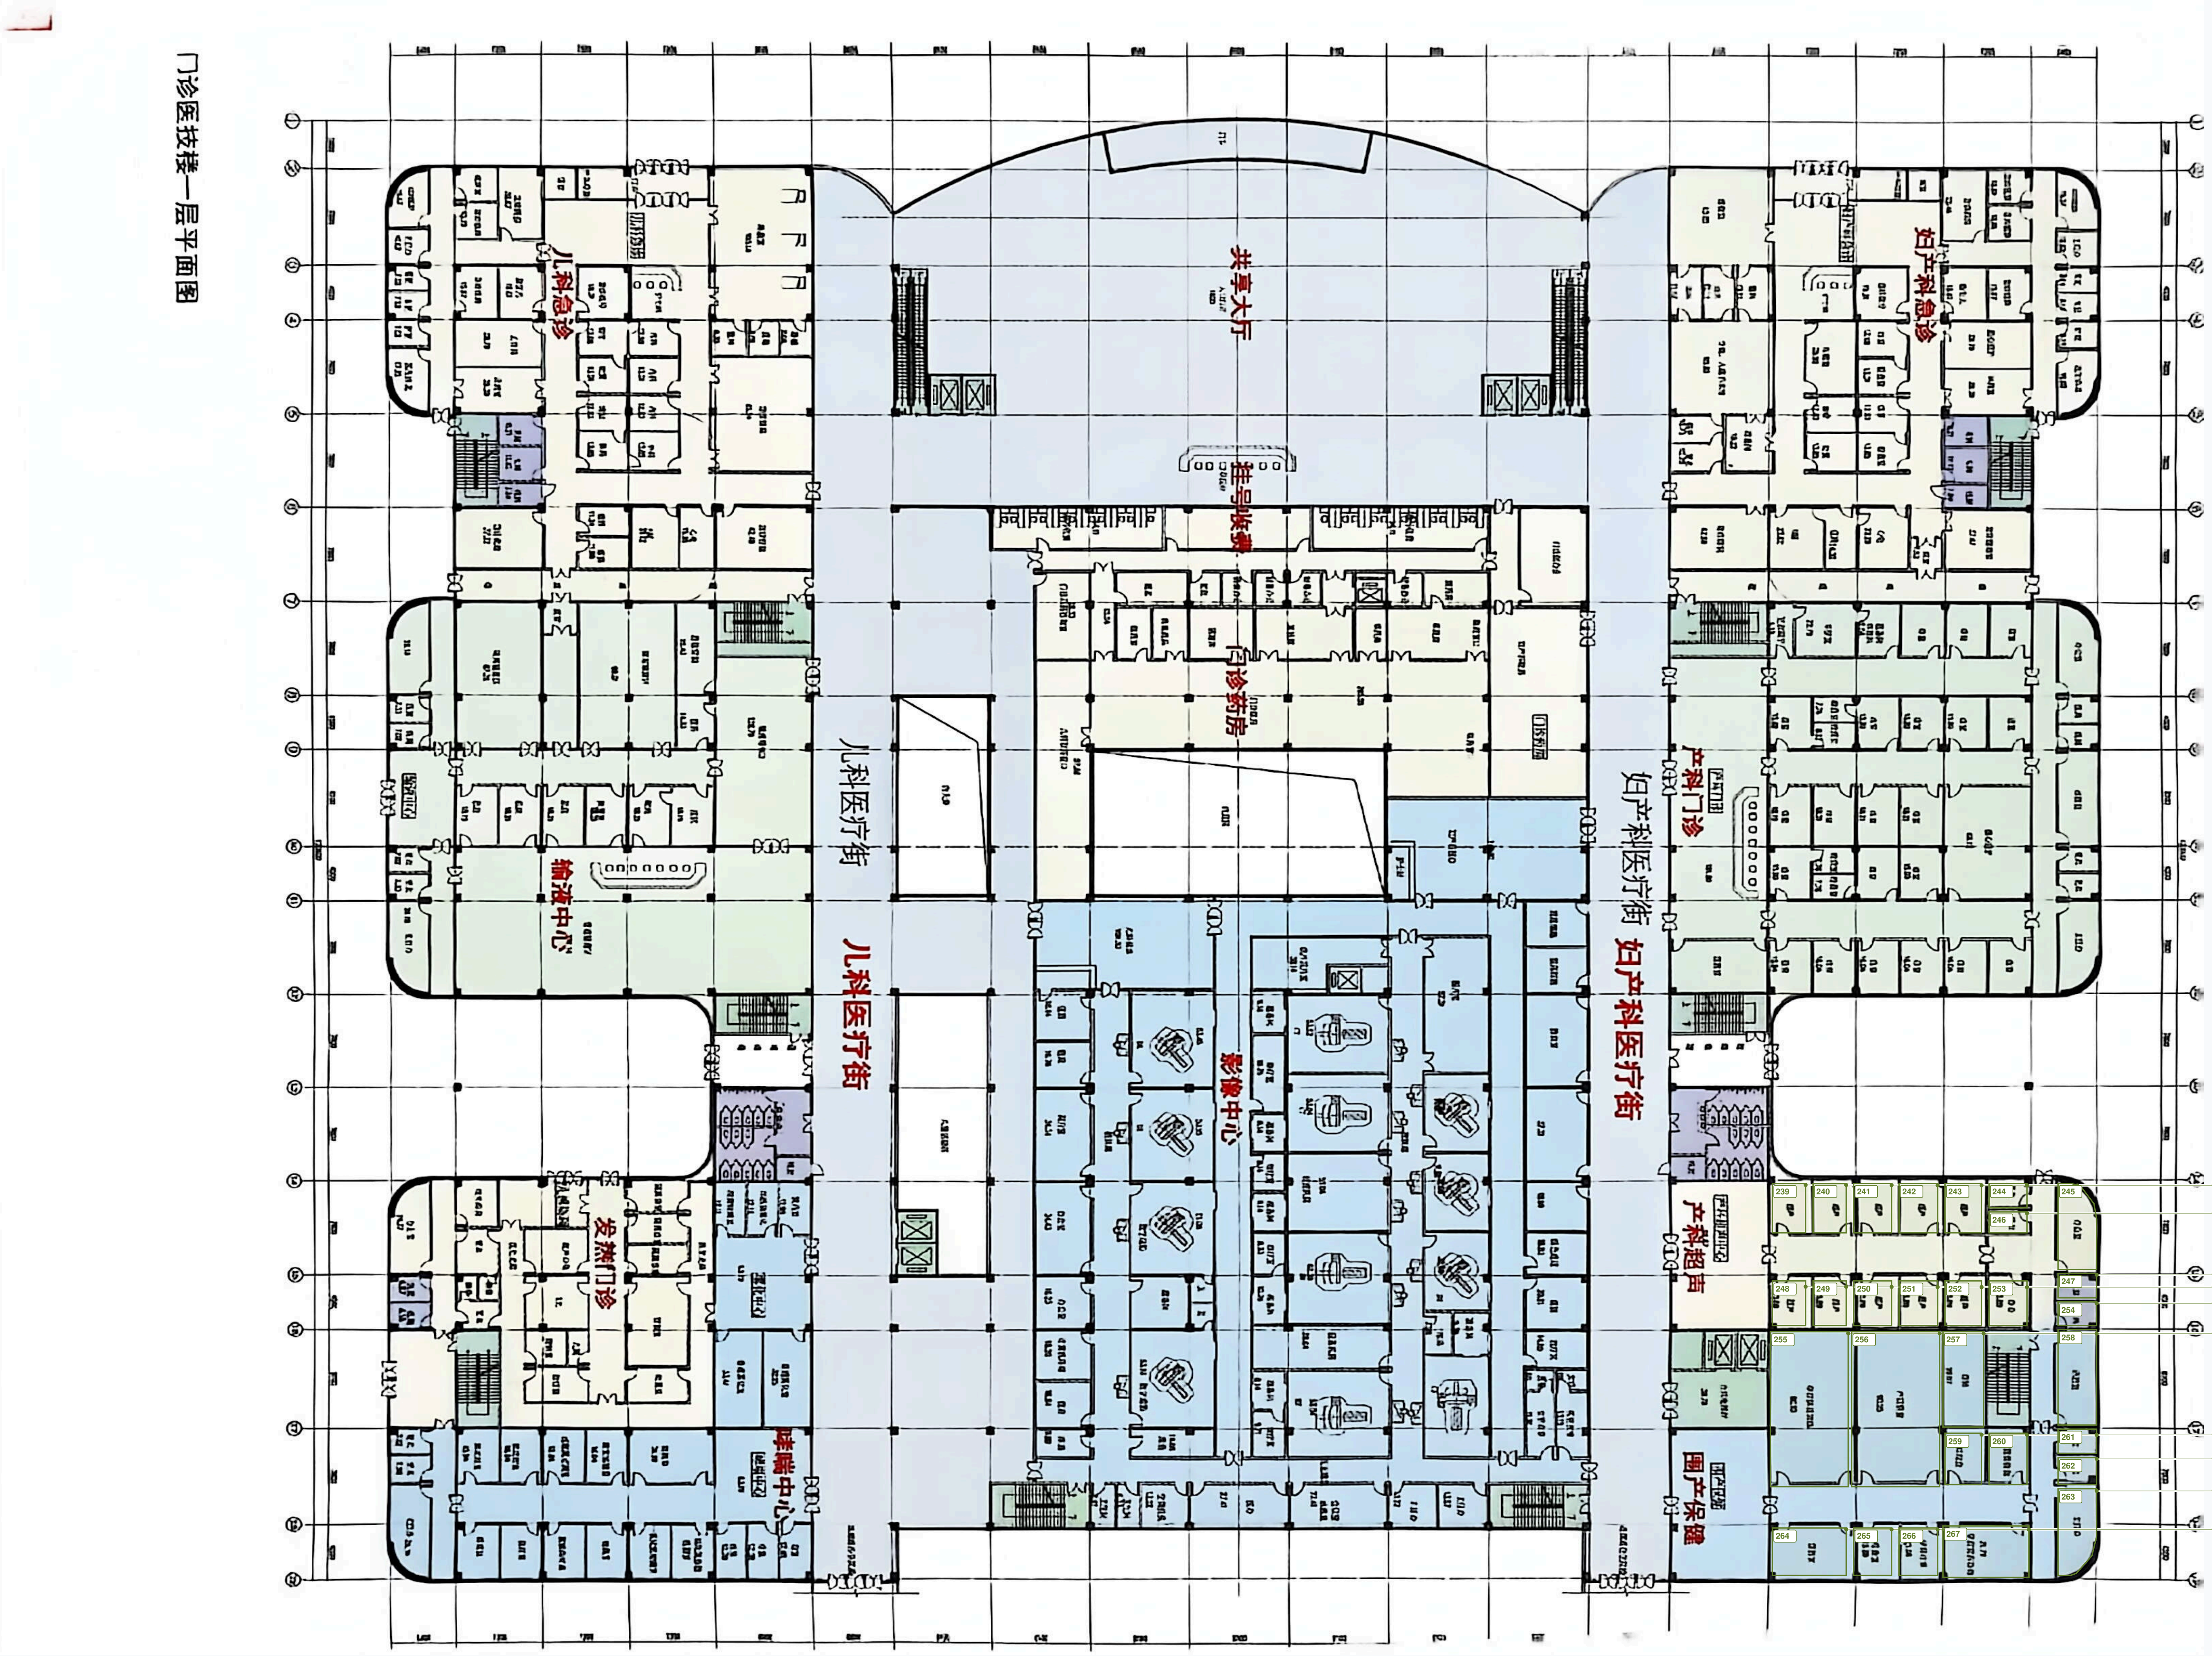

239｜S348｜产科超声与围产保健｜候选：超声检查室 / 诊室（低）
240｜S350｜产科超声与围产保健｜候选：超声检查室 / 诊室（低）
241｜S352｜产科超声与围产保健｜候选：超声检查室 / 诊室（低）
242｜S354｜产科超声与围产保健｜候选：超声检查室 / 诊室（低）
243｜S356｜产科超声与围产保健｜候选：超声检查室 / 诊室（低）
244｜S358｜产科超声与围产保健｜候选：患者准备 / 支持用房（低）
245｜S360｜产科超声与围产保健｜候选：办公室 / 值班室（低）
246｜S361｜产科超声与围产保健｜候选：患者准备 / 支持用房（低）
247｜S368｜产科超声与围产保健｜候选：卫生间 / 更衣室（低）
248｜S362｜产科超声与围产保健｜候选：超声检查室 / 诊室（低）
249｜S363｜产科超声与围产保健｜候选：超声检查室 / 诊室（低）
250｜S364｜产科超声与围产保健｜候选：超声检查室 / 诊室（低）
251｜S365｜产科超声与围产保健｜候选：超声检查室 / 诊室（低）
252｜S366｜产科超声与围产保健｜候选：超声检查室 / 诊室（低）
253｜S367｜产科超声与围产保健｜候选：超声检查室 / 诊室（低）
254｜S369｜产科超声与围产保健｜候选：卫生间 / 更衣室（低）
255｜S371｜产科超声与围产保健｜候选：围产保健检查 / 治疗用房（中）
256｜S372｜产科超声与围产保健｜候选：产后康复 / 保健用房（中）
257｜S373｜产科超声与围产保健｜候选：围产保健检查室 / 宣教室（低）
258｜S375｜产科超声与围产保健｜候选：工作人员支持用房（低）
259｜S376｜产科超声与围产保健｜候选：产后康复 / 保健用房（低）
260｜S378｜产科超声与围产保健｜候选：产后康复 / 保健用房（低）
261｜S379｜产科超声与围产保健｜候选：库房 / 设备用房（低）
262｜S380｜产科超声与围产保健｜候选：库房 / 设备用房（低）
263｜S385｜产科超声与围产保健｜候选：办公室 / 值班室（低）
264｜S386｜产科超声与围产保健｜候选：围产保健诊室 / 检查室（低）
265｜S387｜产科超声与围产保健｜候选：围产保健诊室 / 检查室（低）
266｜S388｜产科超声与围产保健｜候选：围产保健诊室 / 检查室（低）
267｜S389｜产科超声与围产保健｜候选：围产保健检查室 / 保健用房（低）

07号平面｜总图**09**_公共大厅与医疗街｜标注草稿：候选均待确认

共 2 项；核对号先左栏后右栏，各栏自上而下；按“01=名称，02=名称”分批回复。

边栏：核对号｜S编号｜候选用途（把握程度）；依据见同目录核对清单。原图未改动。

268｜S402｜公共大厅与医疗街｜候选：内庭院 / 中庭（是否露天待确认）（中）

269｜S404｜公共大厅与医疗街｜候选：内庭院 / 中庭（是否露天待确认）（中）